
Jardim inteiro, casa embaixo

Escala 1:178. Esquerda e direita como vistas da casa olhando para o bosque. Formas cinza são plantas existentes. Pontos coloridos são os 129 vasos novos.

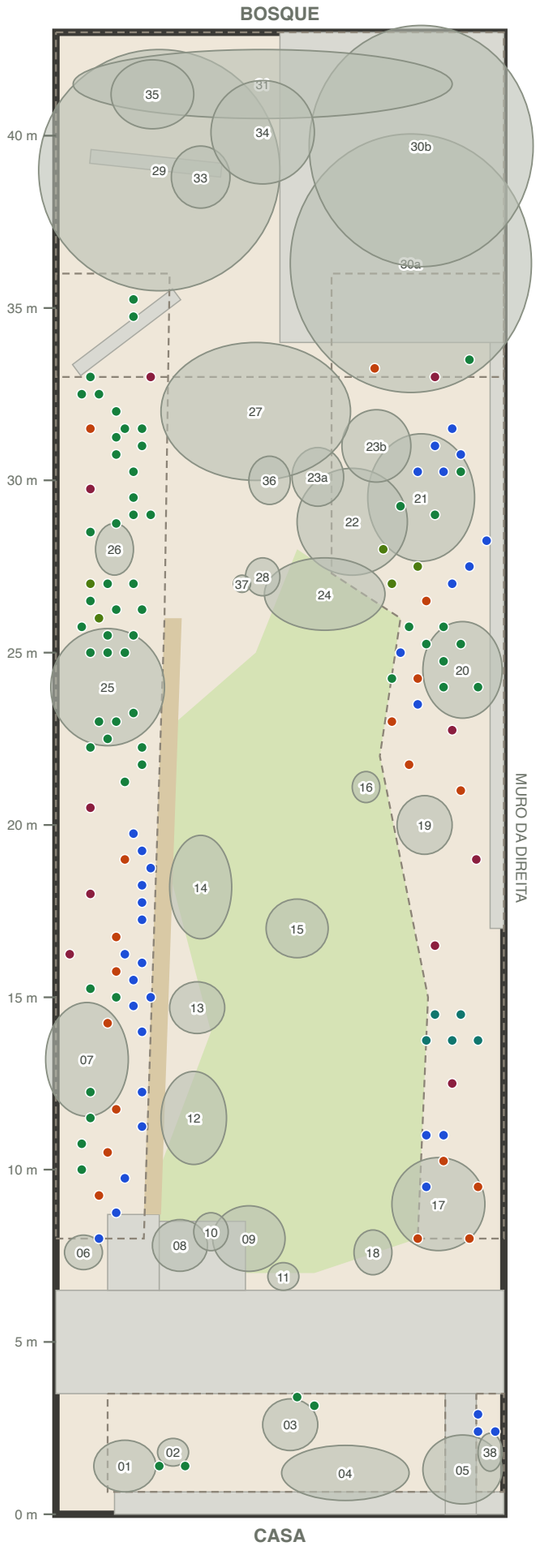

Fundo e canteiros da casa: folha 10

Esquerda: folha 5; direita: folha 9

Esquerda: folha 4; direita: folha 8

Esquerda: folha 3; direita: folha 7

Esquerda: folha 2; direita: folha 6

PLANTAS NOVAS POR TIPO

- Arbusto estrutural: 10 vasos
- Arbusto de flor: 18 vasos
- Perene: 33 vasos
- Gramínea: 5 vasos
- Forração: 58 vasos
- Samambaia: 5 vasos

PLANTAS E ELEMENTOS EXISTENTES (cinza, numerados como no levantamento)

29	Árvore grande, fundo esquerdo
30a	Árvore grande, fundo direito A
30b	Árvore grande, fundo direito B
31	Hera e vegetação do fundo
01	Arbusto dourado, canteiro baixo
02	Arbusto lenhoso podado
03	Arbusto dourado podado
04	Arbustos variegados, canteiro baixo
05	Arbusto dourado, direita baixa
06	Arbusto pequeno junto ao muro esquerdo
07	Eleagno grande
08	Euonymus dourado, floreira esquerda
09	Euonymus dourado, floreira direita
10	Grupo misto na floreira
11	Touceira de folhas longas
12	Acanto e folhas longas
13	Acanto, meio
14	Touceira de folhas longas, mais ao fundo
15	Acanto central
16	Arbusto pequeno no gramado
17	Budleia junto ao terraço
18	Arbusto pequeno junto ao terraço
19	Hipérico (provável)
20	Arvoreta junto ao muro direito
21	Budleia alta
22	Fátsia
23a	Bambu, touceira clara
23b	Bambu, touceira escura
24	Acantos abaixo da fátsia
25	Macieira (provável)
26	Arbusto podado, esquerda
27	Macieira baixa e inclinada
28	Touceira pequena podada
33	Azevinho (provável)
34	Arbusto de frutos laranja
35	Arbusto de folhas brilhantes
36	Fátsia jovem
37	Toco cortado
38	Canteiro do alecrim junto à escada

Como usar este plano

1. Encontre o trecho do canteiro nesta página e vá até a folha dele.
2. Prenda a trena na ponta do muro junto à casa e leia o primeiro número ao longo dele.
3. Estique uma segunda trena em linha reta a partir do muro e leia o segundo número.
4. Coloque o vaso no lugar. Marque o trecho inteiro antes de cavar qualquer coisa.
5. Se um vaso cair sobre uma raiz, deslize-o ao longo do canteiro, não em direção ao caminho ou ao gramado.

ANTES DE CAVAR

As posições vêm de um levantamento por fotos, não de uma medição.
Coloque todos os vasos no lugar, caminhe pelos canteiros e só então cave.


Gerado em 2026-11-05 a partir do levantamento fotográfico (rev. 04) e do pedido de 129 plantas da Palmstead.

Canteiro da esquerda, de 8 a 15 m da casa

A casa fica à ESQUERDA desta folha e o bosque à DIREITA. O MURO DA ESQUERDA corre pela parte de CIMA. Escala 1:25. Ponto = centro do vaso. Círculo claro = espaço de que a planta precisa.

< PARA A CASA

PARA O BOSQUE >

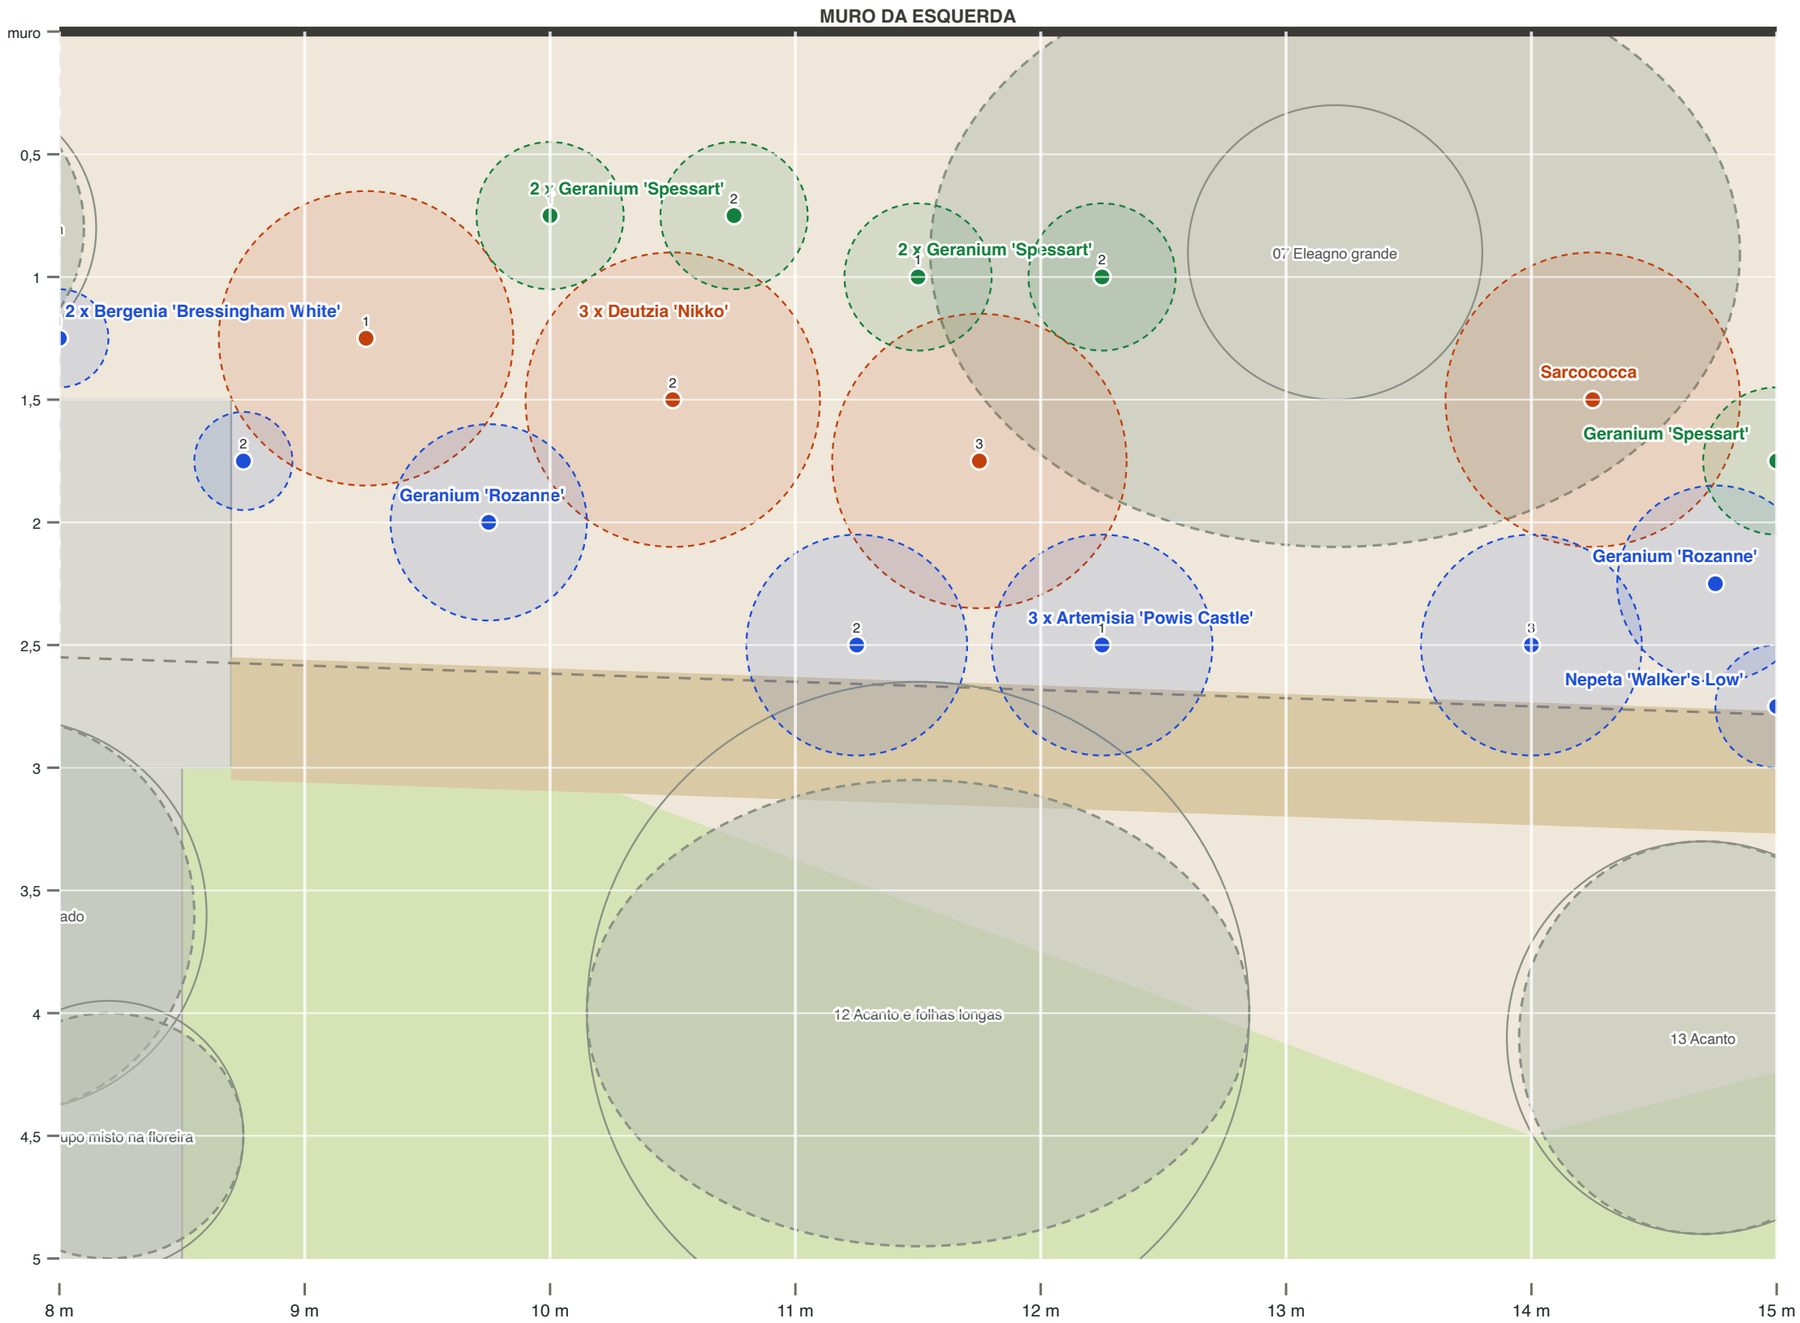

MARCAÇÃO: trena ao longo do muro, depois a partir do muro

2 x Bergenia 'Bressingham White'	
1	8 ao longo, 1,25 do muro
2	8,75 ao longo, 1,75 do muro
3 x Deutzia 'Nikko'	
1	9,25 ao longo, 1,25 do muro
2	10,5 ao longo, 1,5 do muro
3	11,75 ao longo, 1,75 do muro
Geranium 'Rozanne'	9,75 ao longo, 2 do muro
2 x Geranium 'Spessart'	
1	10 ao longo, 0,75 do muro
2	10,75 ao longo, 0,75 do muro
3 x Artemisia 'Powis Castle'	
1	11,25 ao longo, 2,5 do muro
2	12,25 ao longo, 2,5 do muro
3	14 ao longo, 2,5 do muro
2 x Geranium 'Spessart'	
1	11,5 ao longo, 1 do muro
2	12,25 ao longo, 1 do muro
Sarcococca	14,25 ao longo, 1,5 do muro
Geranium 'Rozanne'	14,75 ao longo, 2,25 do muro
Geranium 'Spessart'	15 ao longo, 1,75 do muro
Nepeta 'Walker's Low'	15 ao longo, 2,75 do muro

ANTES DE CAVAR


As posições vêm de um levantamento por fotos, não de uma medição.
Coloque todos os vasos no lugar, caminhe pelos canteiros e só então cave.

Canteiro da esquerda, de 15 a 22 m da casa

A casa fica à ESQUERDA desta folha e o bosque à DIREITA. O MURO DA ESQUERDA corre pela parte de CIMA. Escala 1:25. Ponto = centro do vaso. Círculo claro = espaço de que a planta precisa.

< PARA A CASA

PARA O BOSQUE >

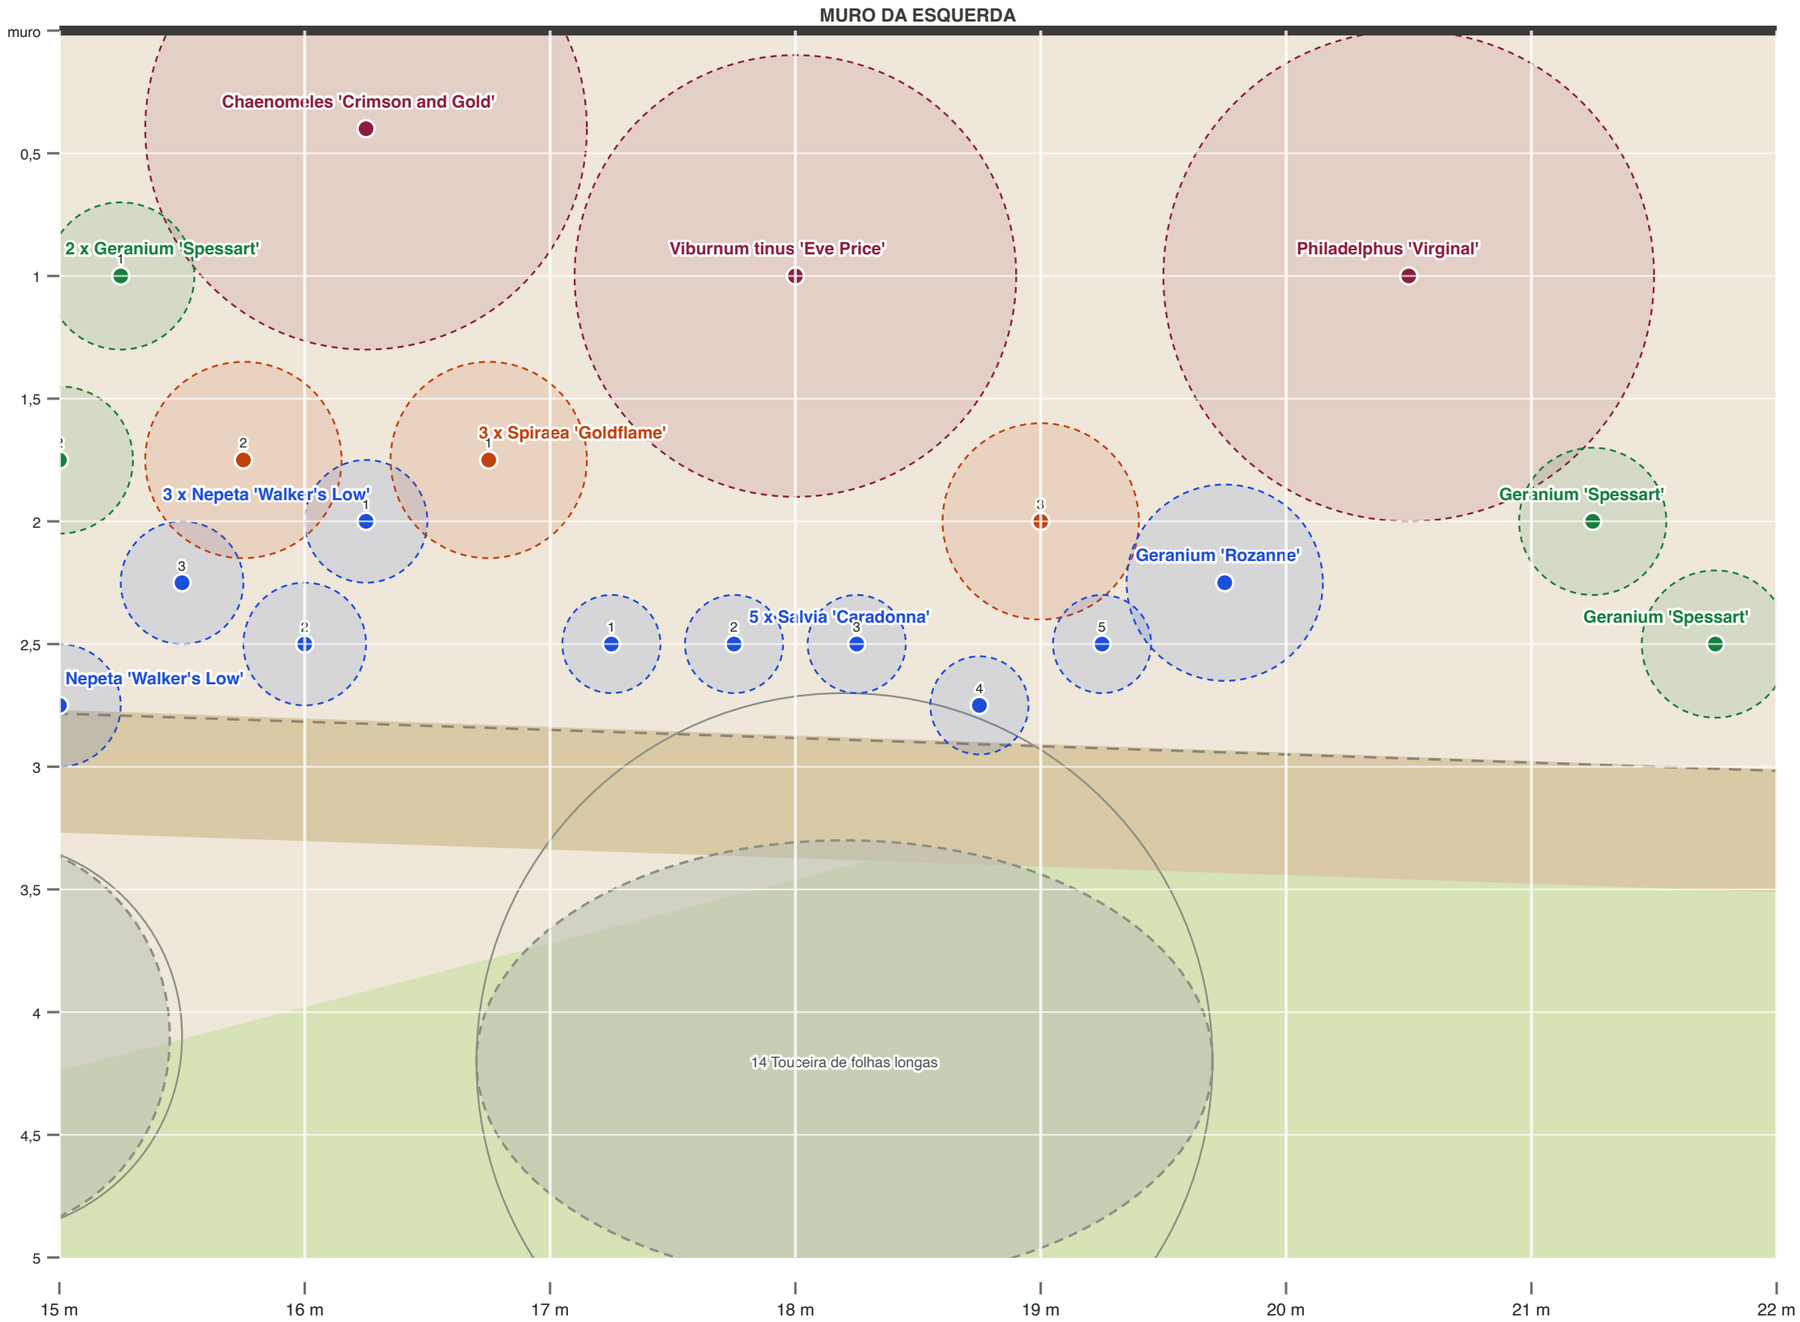

MARCAÇÃO: trena ao longo do muro, depois a partir do muro

2 x Geranium 'Spessart'	
1	15 ao longo, 1,75 do muro
2	15,25 ao longo, 1 do muro
Nepeta 'Walker's Low'	15 ao longo, 2,75 do muro
3 x Nepeta 'Walker's Low'	
1	15,5 ao longo, 2,25 do muro
2	16 ao longo, 2,5 do muro
3	16,25 ao longo, 2 do muro
3 x Spiraea 'Goldflame'	
1	15,75 ao longo, 1,75 do muro
2	16,75 ao longo, 1,75 do muro
3	19 ao longo, 2 do muro
Chaenomeles 'Crimson and Gold'	16,25 ao longo, 0,4 do muro
5 x Salvia 'Caradonna'	
1	17,25 ao longo, 2,5 do muro
2	17,75 ao longo, 2,5 do muro
3	18,25 ao longo, 2,5 do muro
4	18,75 ao longo, 2,75 do muro
5	19,25 ao longo, 2,5 do muro
Viburnum tinus 'Eve Price'	18 ao longo, 1 do muro
Geranium 'Rozanne'	19,75 ao longo, 2,25 do muro
Philadelphus 'Virginal'	20,5 ao longo, 1 do muro
Geranium 'Spessart'	21,25 ao longo, 2 do muro
Geranium 'Spessart'	21,75 ao longo, 2,5 do muro

ANTES DE CAVAR


As posições vêm de um levantamento por fotos, não de uma medição.
Coloque todos os vasos no lugar, caminhe pelos canteiros e só então cave.

Canteiro da esquerda, de 22 a 29 m da casa

A casa fica à ESQUERDA desta folha e o bosque à DIREITA. O MURO DA ESQUERDA corre pela parte de CIMA. Escala 1:25. Ponto = centro do vaso. Círculo claro = espaço de que a planta precisa.

< PARA A CASA

PARA O BOSQUE >

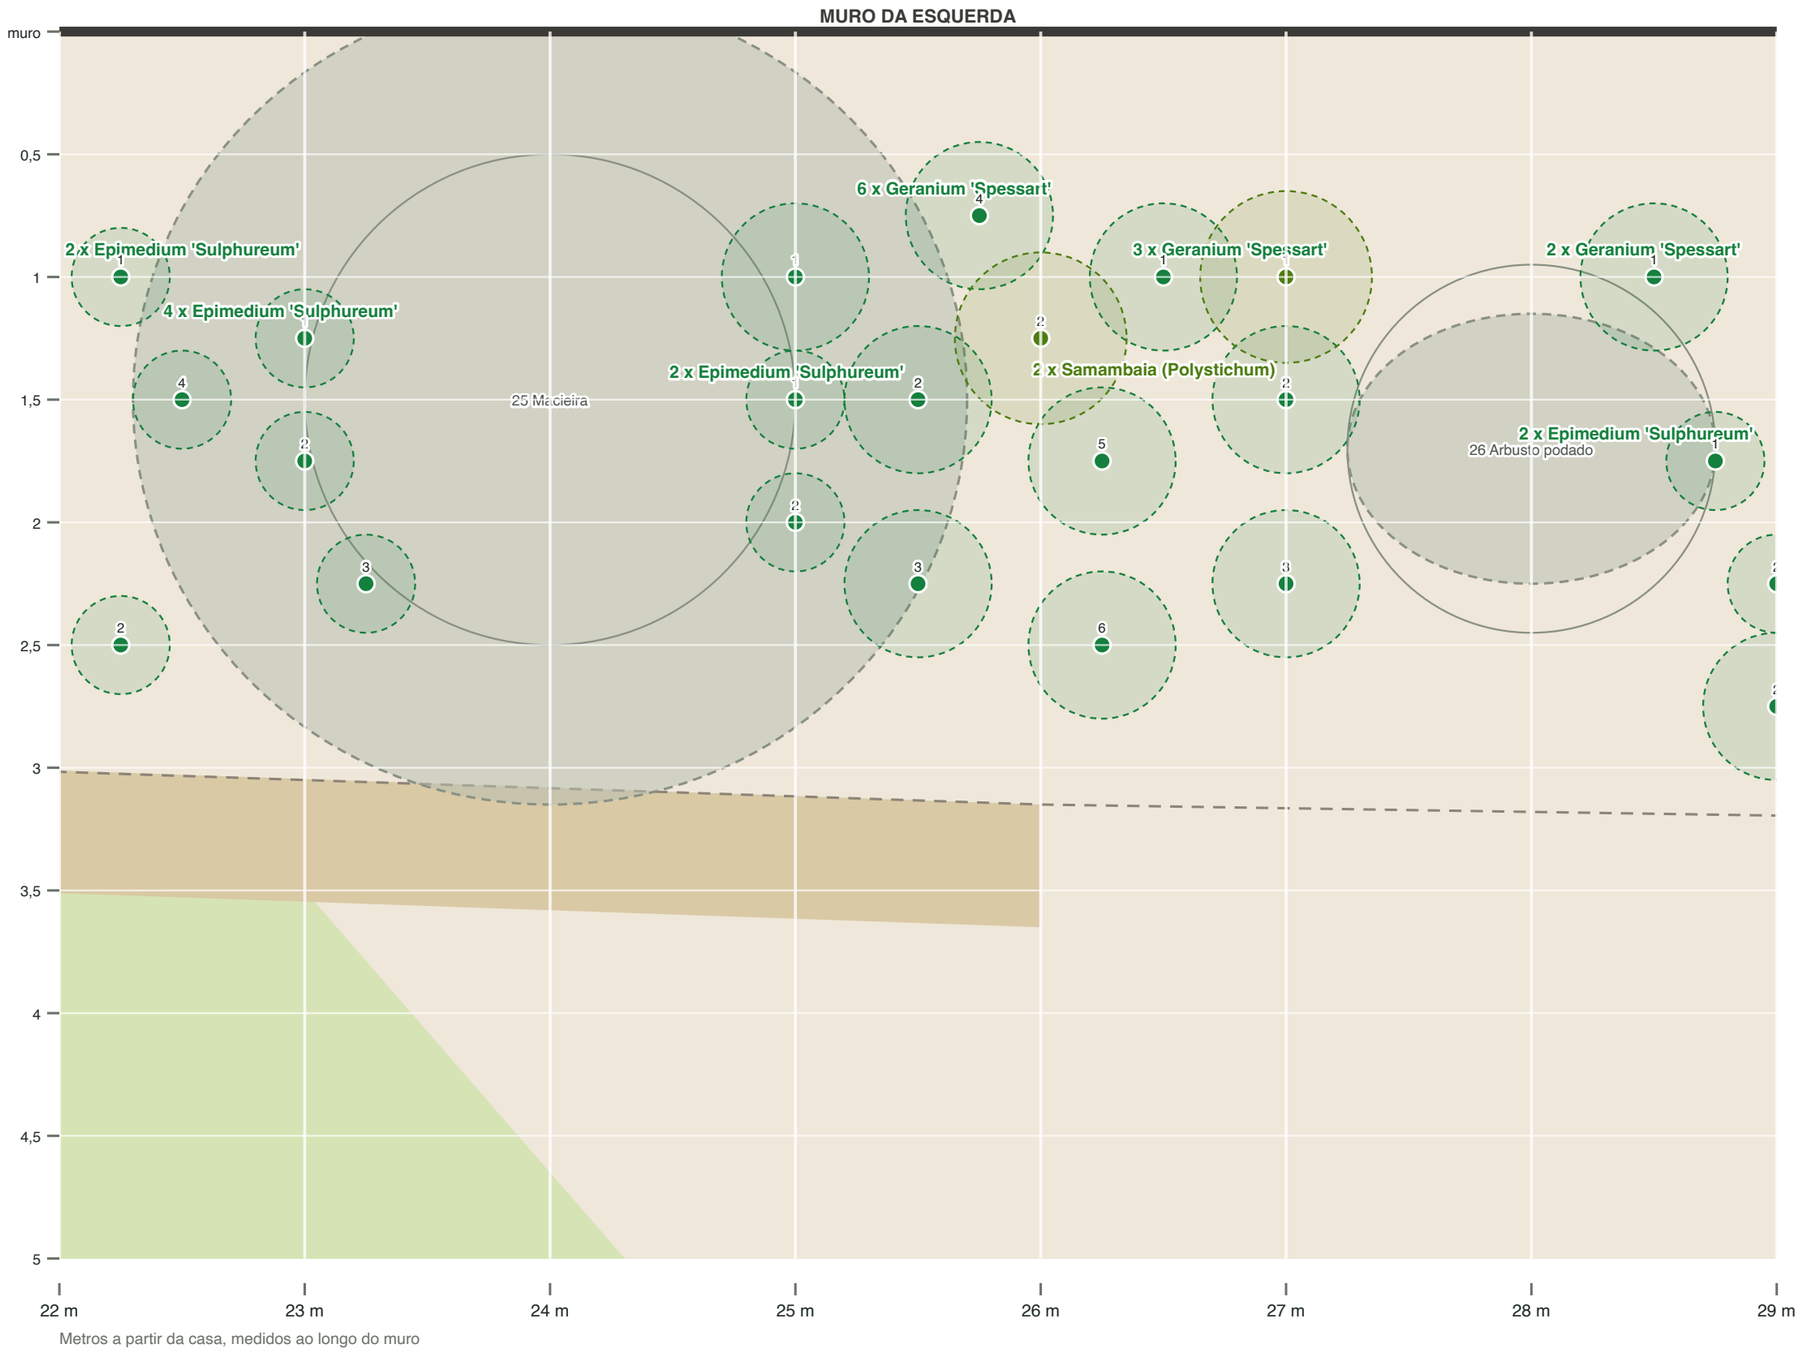

MARCAÇÃO: trena ao longo do muro, depois a partir do muro

- **2 x Epimedium 'Sulphureum'**
  - 1 — 22,25 ao longo, 1 do muro
  - 2 — 22,25 ao longo, 2,5 do muro
- **4 x Epimedium 'Sulphureum'**
  - 1 — 22,5 ao longo, 1,5 do muro
  - 2 — 23 ao longo, 1,25 do muro
  - 3 — 23 ao longo, 1,75 do muro
  - 4 — 23,25 ao longo, 2,25 do muro
- **6 x Geranium 'Spessart'**
  - 1 — 25 ao longo, 1 do muro
  - 2 — 25,5 ao longo, 1,5 do muro
  - 3 — 25,5 ao longo, 2,25 do muro
  - 4 — 25,75 ao longo, 0,75 do muro
  - 5 — 26,25 ao longo, 1,75 do muro
  - 6 — 26,25 ao longo, 2,5 do muro
- **2 x Epimedium 'Sulphureum'**
  - 1 — 25 ao longo, 1,5 do muro
  - 2 — 25 ao longo, 2 do muro
- **2 x Samambaia (Polystichum)**
  - 1 — 26 ao longo, 1,25 do muro
  - 2 — 27 ao longo, 1 do muro
- **3 x Geranium 'Spessart'**
  - 1 — 26,5 ao longo, 1 do muro
  - 2 — 27 ao longo, 1,5 do muro
  - 3 — 27 ao longo, 2,25 do muro
- **2 x Geranium 'Spessart'**
  - 1 — 28,5 ao longo, 1 do muro
  - 2 — 29 ao longo, 2,75 do muro
- **2 x Epimedium 'Sulphureum'**
  - 1 — 28,75 ao longo, 1,75 do muro
  - 2 — 29 ao longo, 2,25 do muro

ANTES DE CAVAR


As posições vêm de um levantamento por fotos, não de uma medição.
Coloque todos os vasos no lugar, caminhe pelos canteiros e só então cave.

Canteiro da esquerda, de 29 a 36 m da casa

A casa fica à ESQUERDA desta folha e o bosque à DIREITA. O MURO DA ESQUERDA corre pela parte de CIMA. Escala 1:25. Ponto = centro do vaso. Círculo claro = espaço de que a planta precisa.

< PARA A CASA

PARA O BOSQUE >

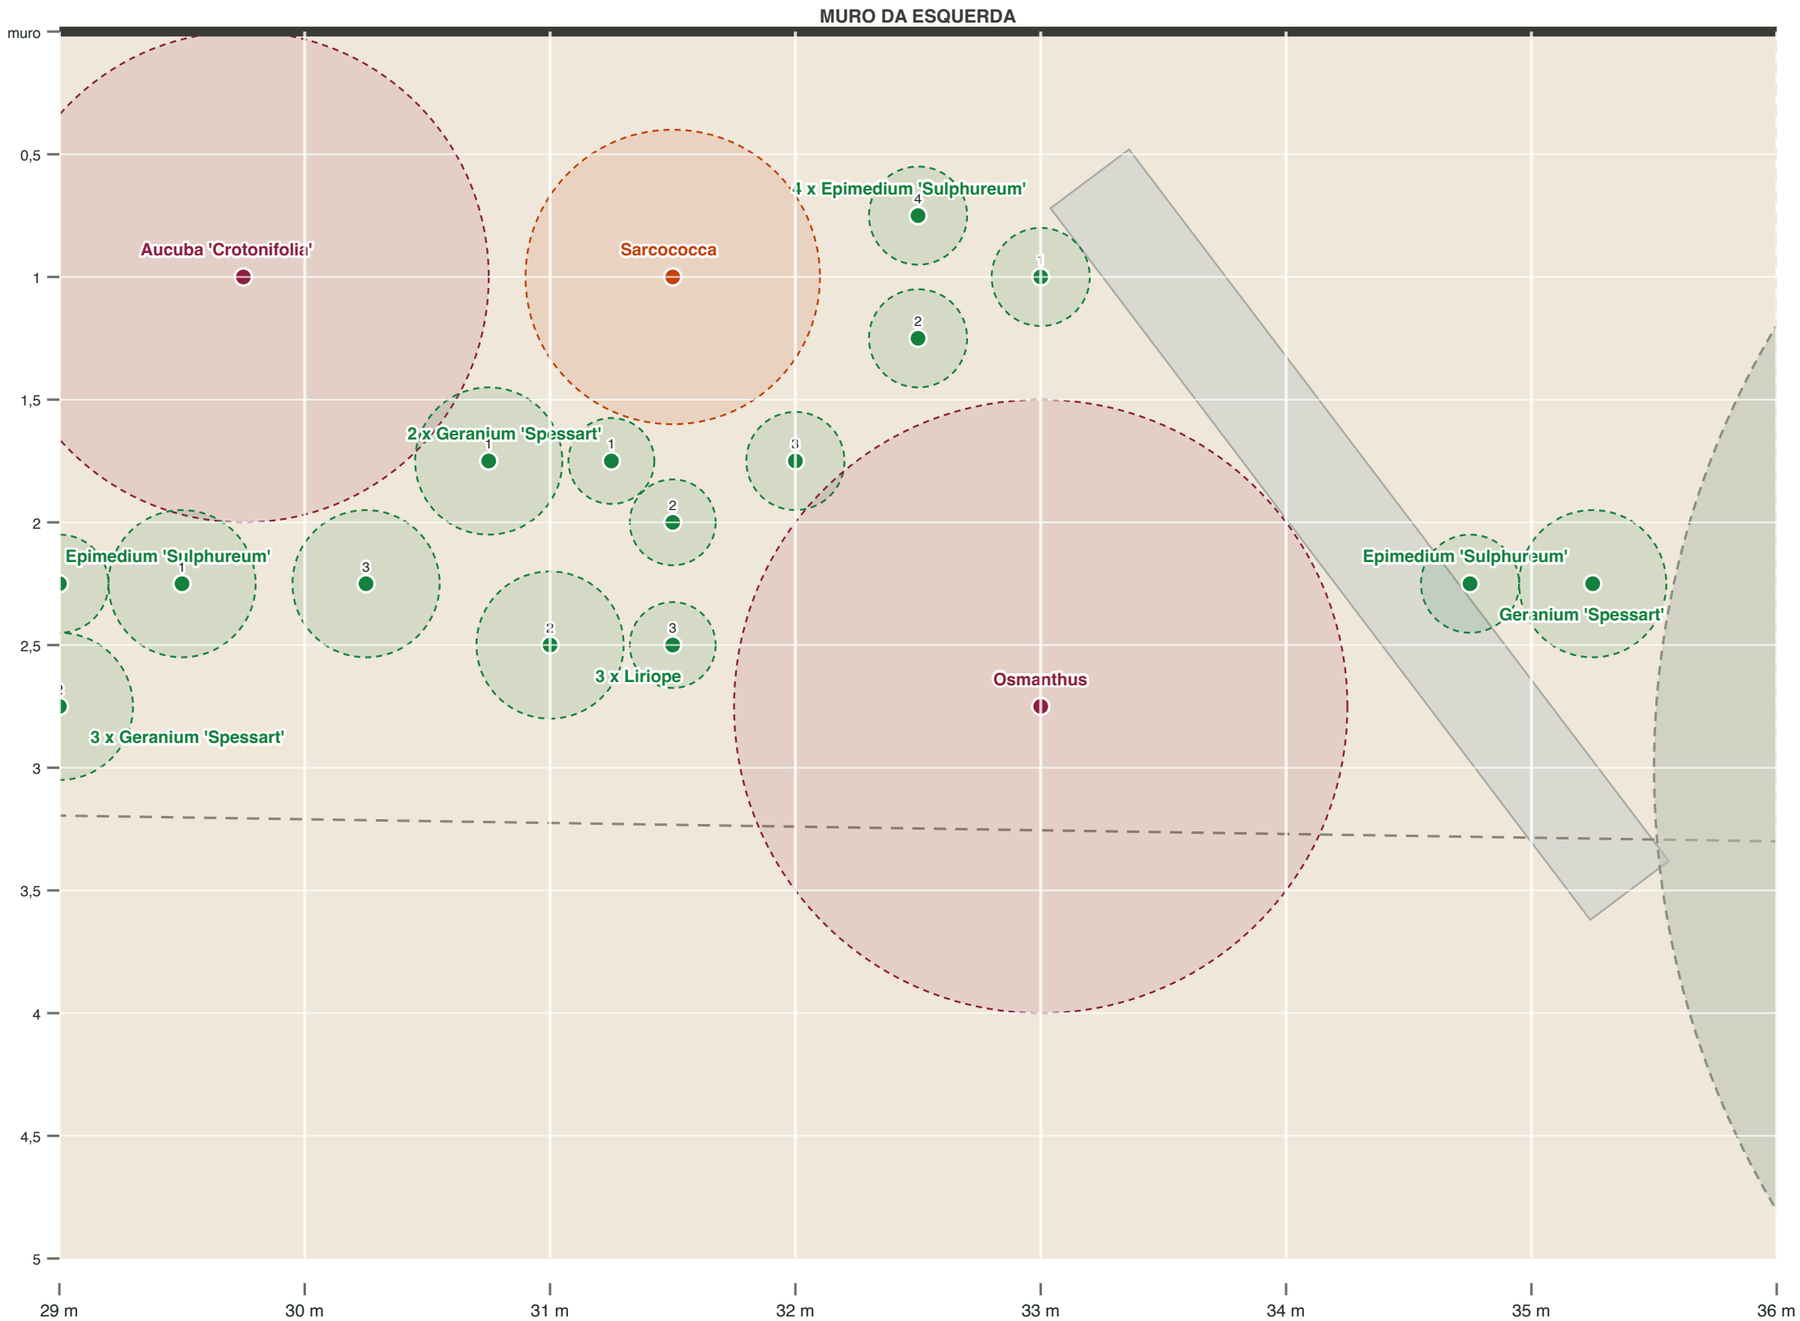

MARCAÇÃO: trena ao longo do muro, depois a partir do muro

Epimedium 'Sulphureum'	29 ao longo, 2,25 do muro
3 x Geranium 'Spessart'	
1	29 ao longo, 2,75 do muro
2	29,5 ao longo, 2,25 do muro
3	30,25 ao longo, 2,25 do muro
Aucuba 'Crotonifolia'	29,75 ao longo, 1 do muro
2 x Geranium 'Spessart'	
1	30,75 ao longo, 1,75 do muro
2	31 ao longo, 2,5 do muro
3 x Liriope	
1	31,25 ao longo, 1,75 do muro
2	31,5 ao longo, 2 do muro
3	31,5 ao longo, 2,5 do muro
Sarcococca	31,5 ao longo, 1 do muro
4 x Epimedium 'Sulphureum'	
1	32 ao longo, 1,75 do muro
2	32,5 ao longo, 0,75 do muro
3	32,5 ao longo, 1,25 do muro
4	33 ao longo, 1 do muro
Osmanthus	33 ao longo, 2,75 do muro
Epimedium 'Sulphureum'	34,75 ao longo, 2,25 do muro
Geranium 'Spessart'	35,25 ao longo, 2,25 do muro

ANTES DE CAVAR


As posições vêm de um levantamento por fotos, não de uma medição.
Coloque todos os vasos no lugar, caminhe pelos canteiros e só então cave.

Canteiro da direita, de 8 a 15 m da casa

A casa fica à ESQUERDA desta folha e o bosque à DIREITA. O MURO DA DIREITA corre pela parte de BAIXO. Escala 1:25. Ponto = centro do vaso. Círculo claro = espaço de que a planta precisa.

< PARA A CASA

PARA O BOSQUE >

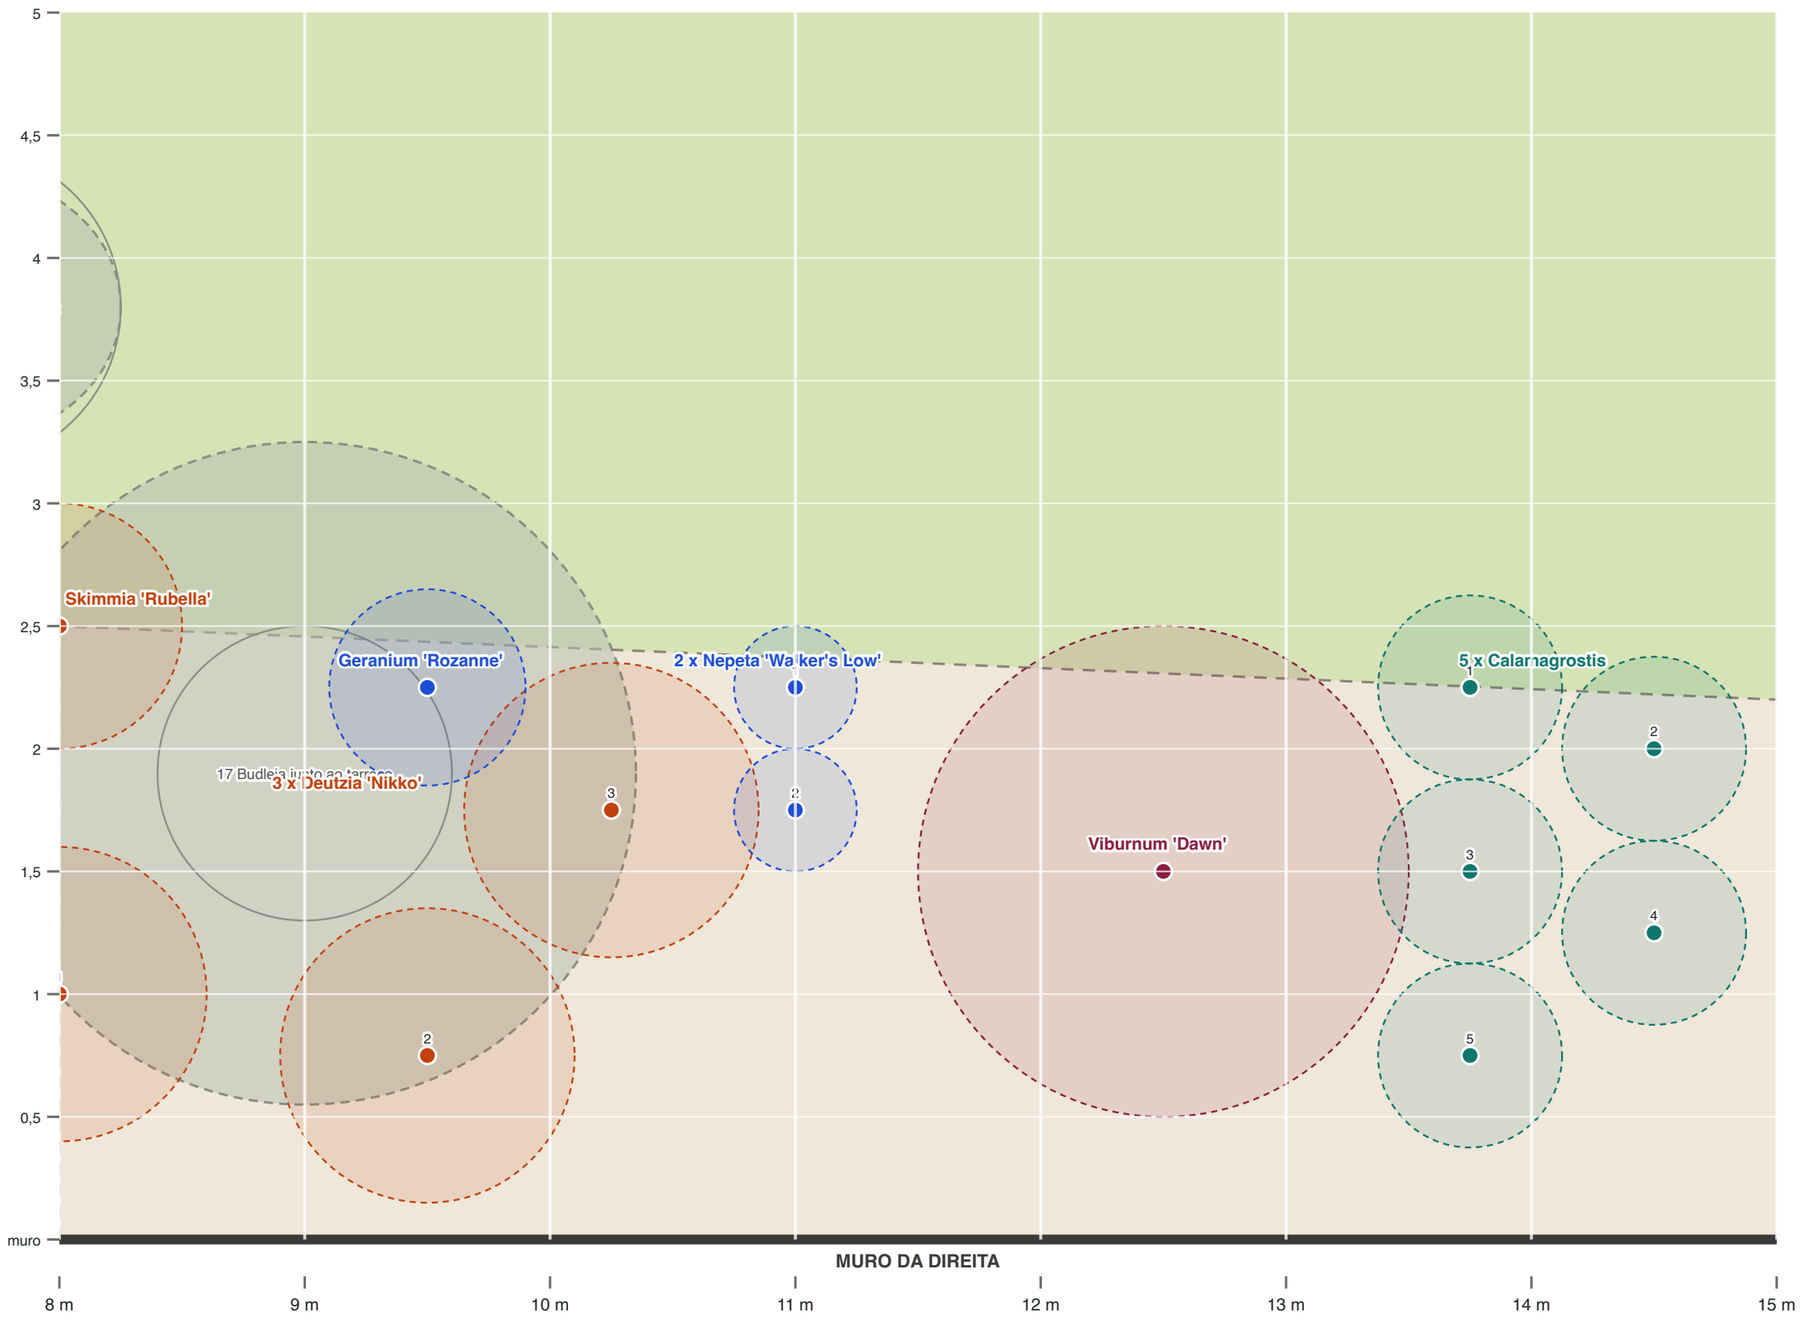

MARCAÇÃO: trena ao longo do muro, depois a partir do muro

Skimmia 'Rubella'	8 ao longo, 2,5 do muro
3 x Deutzia 'Nikko'	
1	8 ao longo, 1 do muro
2	9,5 ao longo, 0,75 do muro
3	10,25 ao longo, 1,75 do muro
Geranium 'Rozanne'	9,5 ao longo, 2,25 do muro
2 x Nepeta 'Walker's Low'	
1	11 ao longo, 2,25 do muro
2	11 ao longo, 1,75 do muro
Viburnum 'Dawn'	12,5 ao longo, 1,5 do muro
5 x Calamagrostis	
1	13,75 ao longo, 2,25 do muro
2	13,75 ao longo, 1,5 do muro
3	13,75 ao longo, 0,75 do muro
4	14,5 ao longo, 2 do muro
5	14,5 ao longo, 1,25 do muro

ANTES DE CAVAR


As posições vêm de um levantamento por fotos, não de uma medição.
Coloque todos os vasos no lugar, caminhe pelos canteiros e só então cave.

Canteiro da direita, de 15 a 22 m da casa

A casa fica à ESQUERDA desta folha e o bosque à DIREITA. O MURO DA DIREITA corre pela parte de BAIXO. Escala 1:25. Ponto = centro do vaso. Círculo claro = espaço de que a planta precisa.

< PARA A CASA

PARA O BOSQUE >

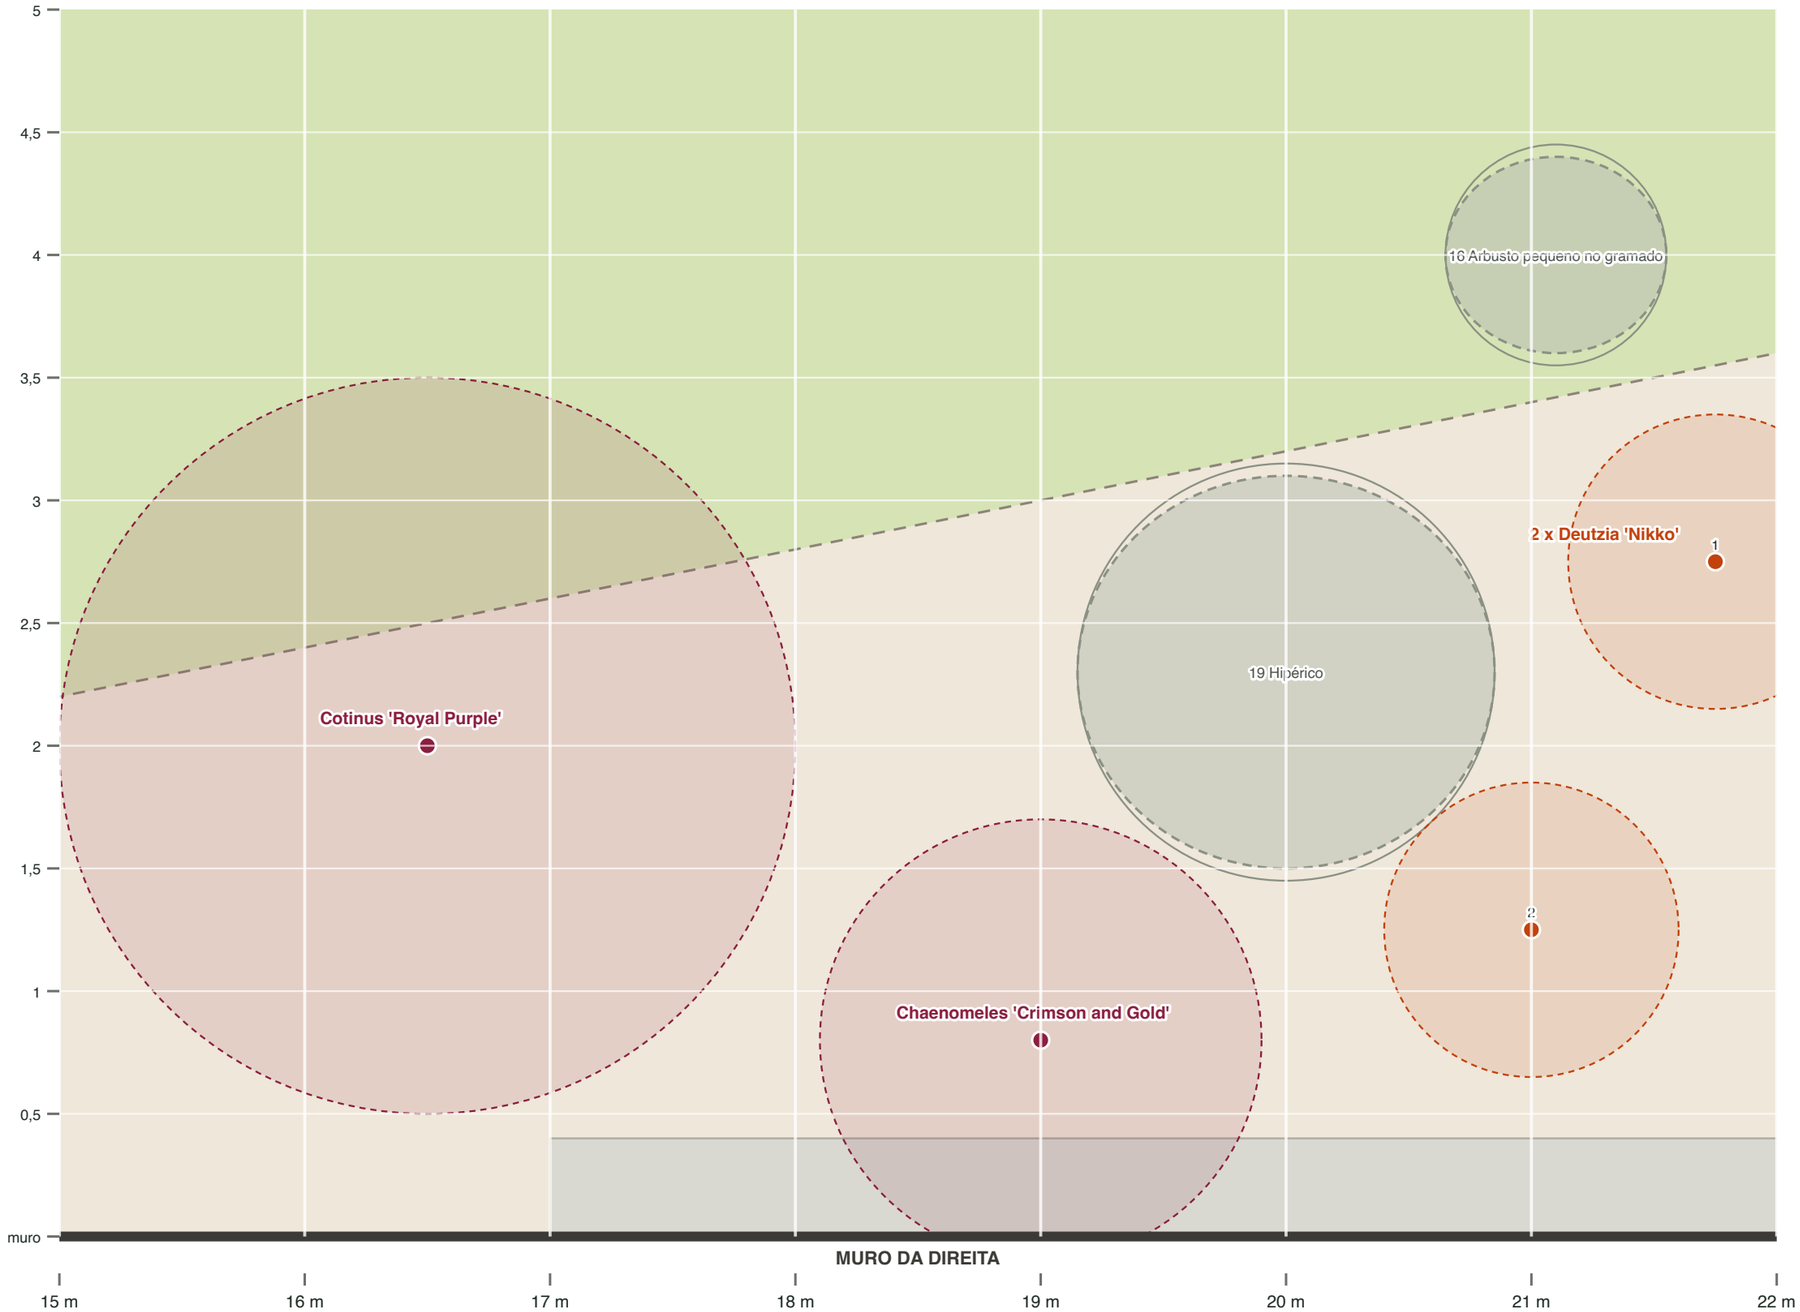

Metros a partir da casa, medidos ao longo do muro

MARCAÇÃO: trena ao longo do muro, depois a partir do muro

Cotinus 'Royal Purple'	16,5 ao longo, 2 do muro
Chaenomeles 'Crimson and Gold'	19 ao longo, 0,8 do muro
2 x Deutzia 'Nikko'	
1	21 ao longo, 1,25 do muro
2	21,75 ao longo, 2,75 do muro

ANTES DE CAVAR


As posições vêm de um levantamento por fotos, não de uma medição.
Coloque todos os vasos no lugar, caminhe pelos canteiros e só então cave.

Canteiro da direita, de 22 a 29 m da casa

A casa fica à ESQUERDA desta folha e o bosque à DIREITA. O MURO DA DIREITA corre pela parte de BAIXO. Escala 1:25. Ponto = centro do vaso. Círculo claro = espaço de que a planta precisa.

< PARA A CASA

PARA O BOSQUE >

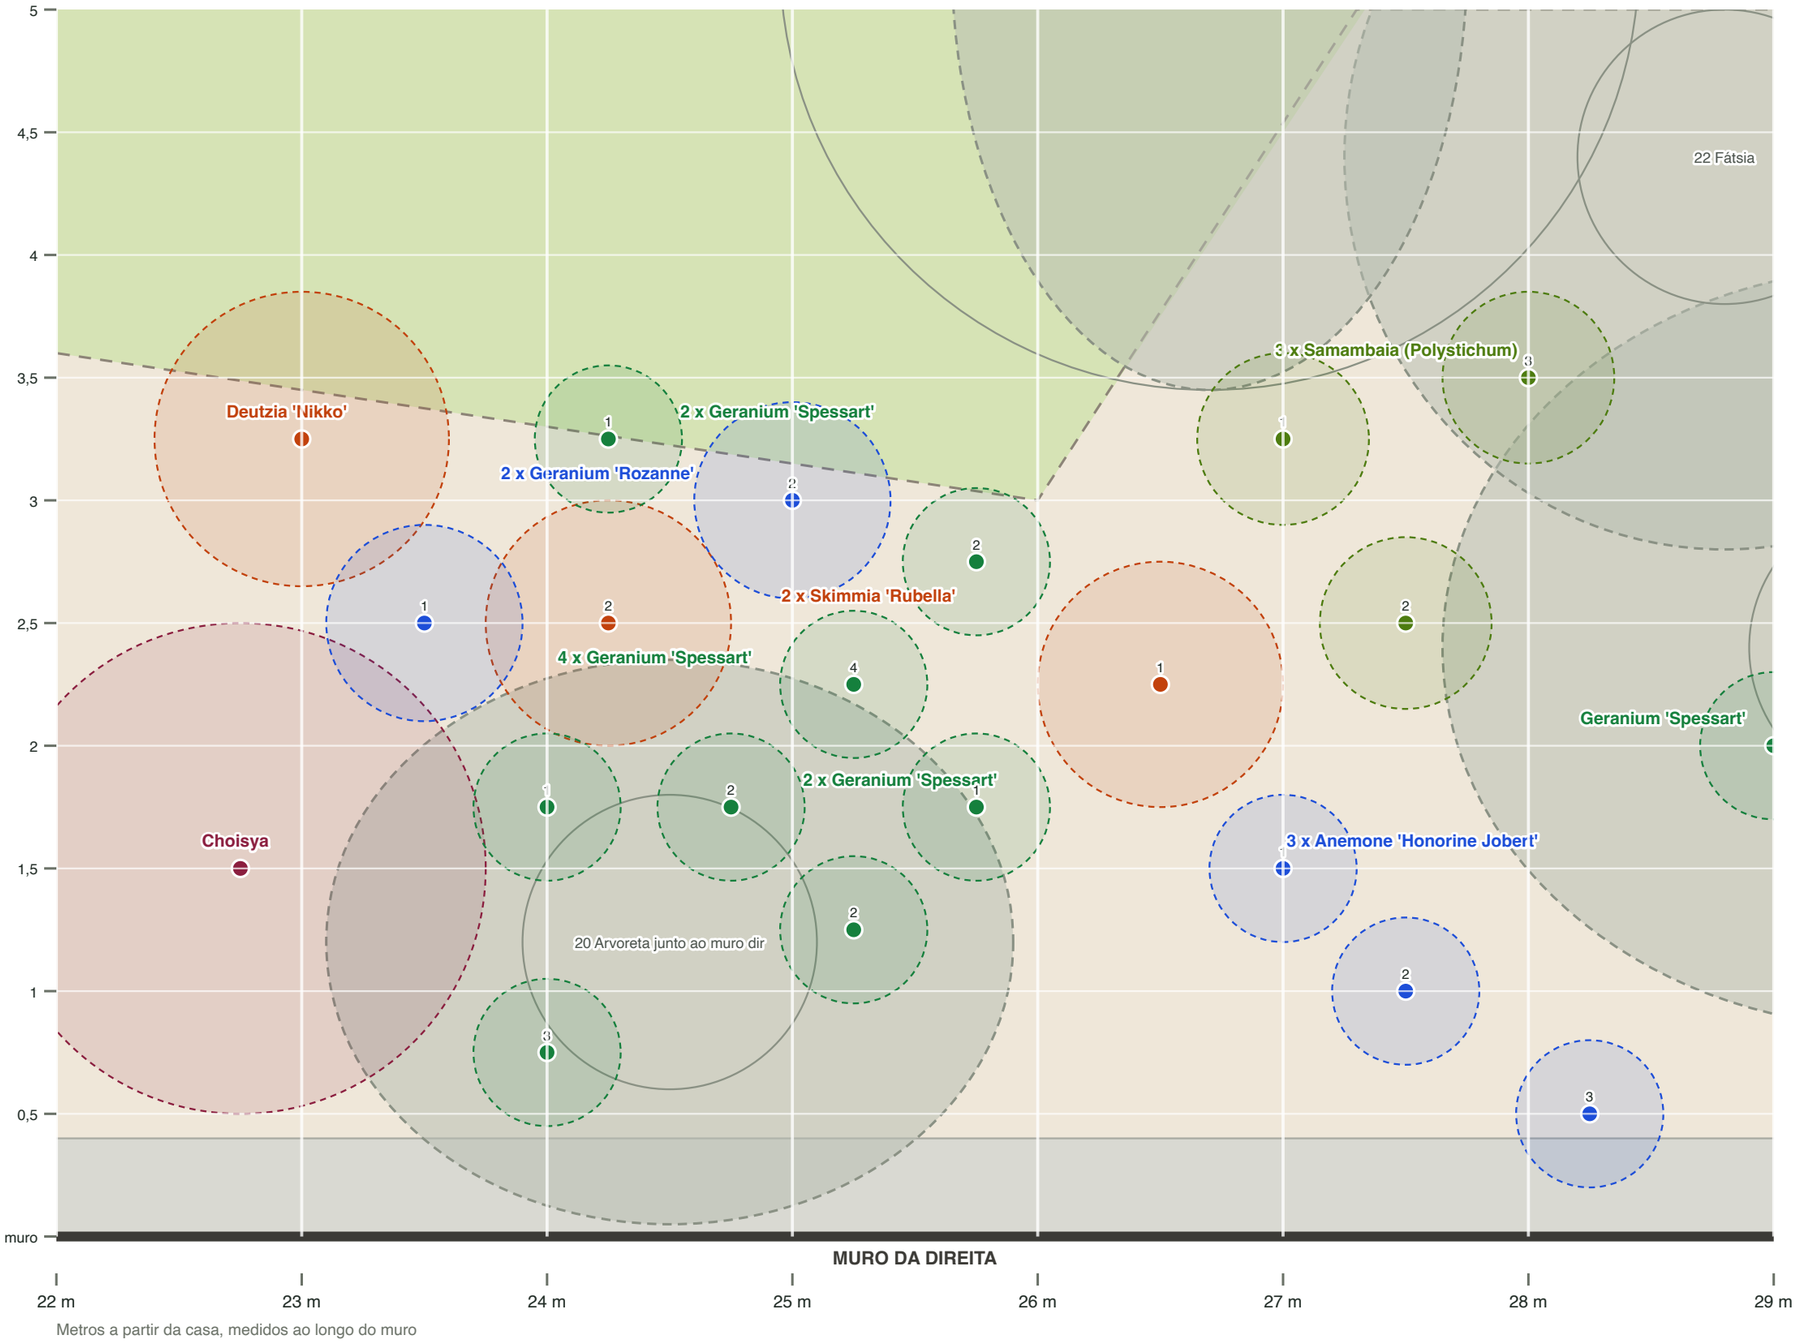

MARCAÇÃO: trena ao longo do muro, depois a partir do muro

Choisya	22,75 ao longo, 1,5 do muro
Deutzia 'Nikko'	23 ao longo, 3,25 do muro
2 x Geranium 'Rozanne'	
1	23,5 ao longo, 2,5 do muro
2	25 ao longo, 3 do muro
4 x Geranium 'Spessart'	
1	24 ao longo, 1,75 do muro
2	24 ao longo, 0,75 do muro
3	24,75 ao longo, 1,75 do muro
4	25,25 ao longo, 2,25 do muro
2 x Geranium 'Spessart'	
1	24,25 ao longo, 3,25 do muro
2	25,75 ao longo, 2,75 do muro
2 x Skimmia 'Rubella'	
1	24,25 ao longo, 2,5 do muro
2	26,5 ao longo, 2,25 do muro
2 x Geranium 'Spessart'	
1	25,25 ao longo, 1,25 do muro
2	25,75 ao longo, 1,75 do muro
3 x Samambaia (Polystichum)	
1	27 ao longo, 3,25 do muro
2	27,5 ao longo, 2,5 do muro
3	28 ao longo, 3,5 do muro
3 x Anemone 'Honorine Jobert'	
1	27 ao longo, 1,5 do muro
2	27,5 ao longo, 1 do muro
3	28,25 ao longo, 0,5 do muro
Geranium 'Spessart'	29 ao longo, 2 do muro

ANTES DE CAVAR


As posições vêm de um levantamento por fotos, não de uma medição.
Coloque todos os vasos no lugar, caminhe pelos canteiros e só então cave.

Canteiro da direita, de 29 a 36 m da casa

A casa fica à ESQUERDA desta folha e o bosque à DIREITA. O MURO DA DIREITA corre pela parte de BAIXO. Escala 1:25. Ponto = centro do vaso. Círculo claro = espaço de que a planta precisa.

< PARA A CASA

PARA O BOSQUE >

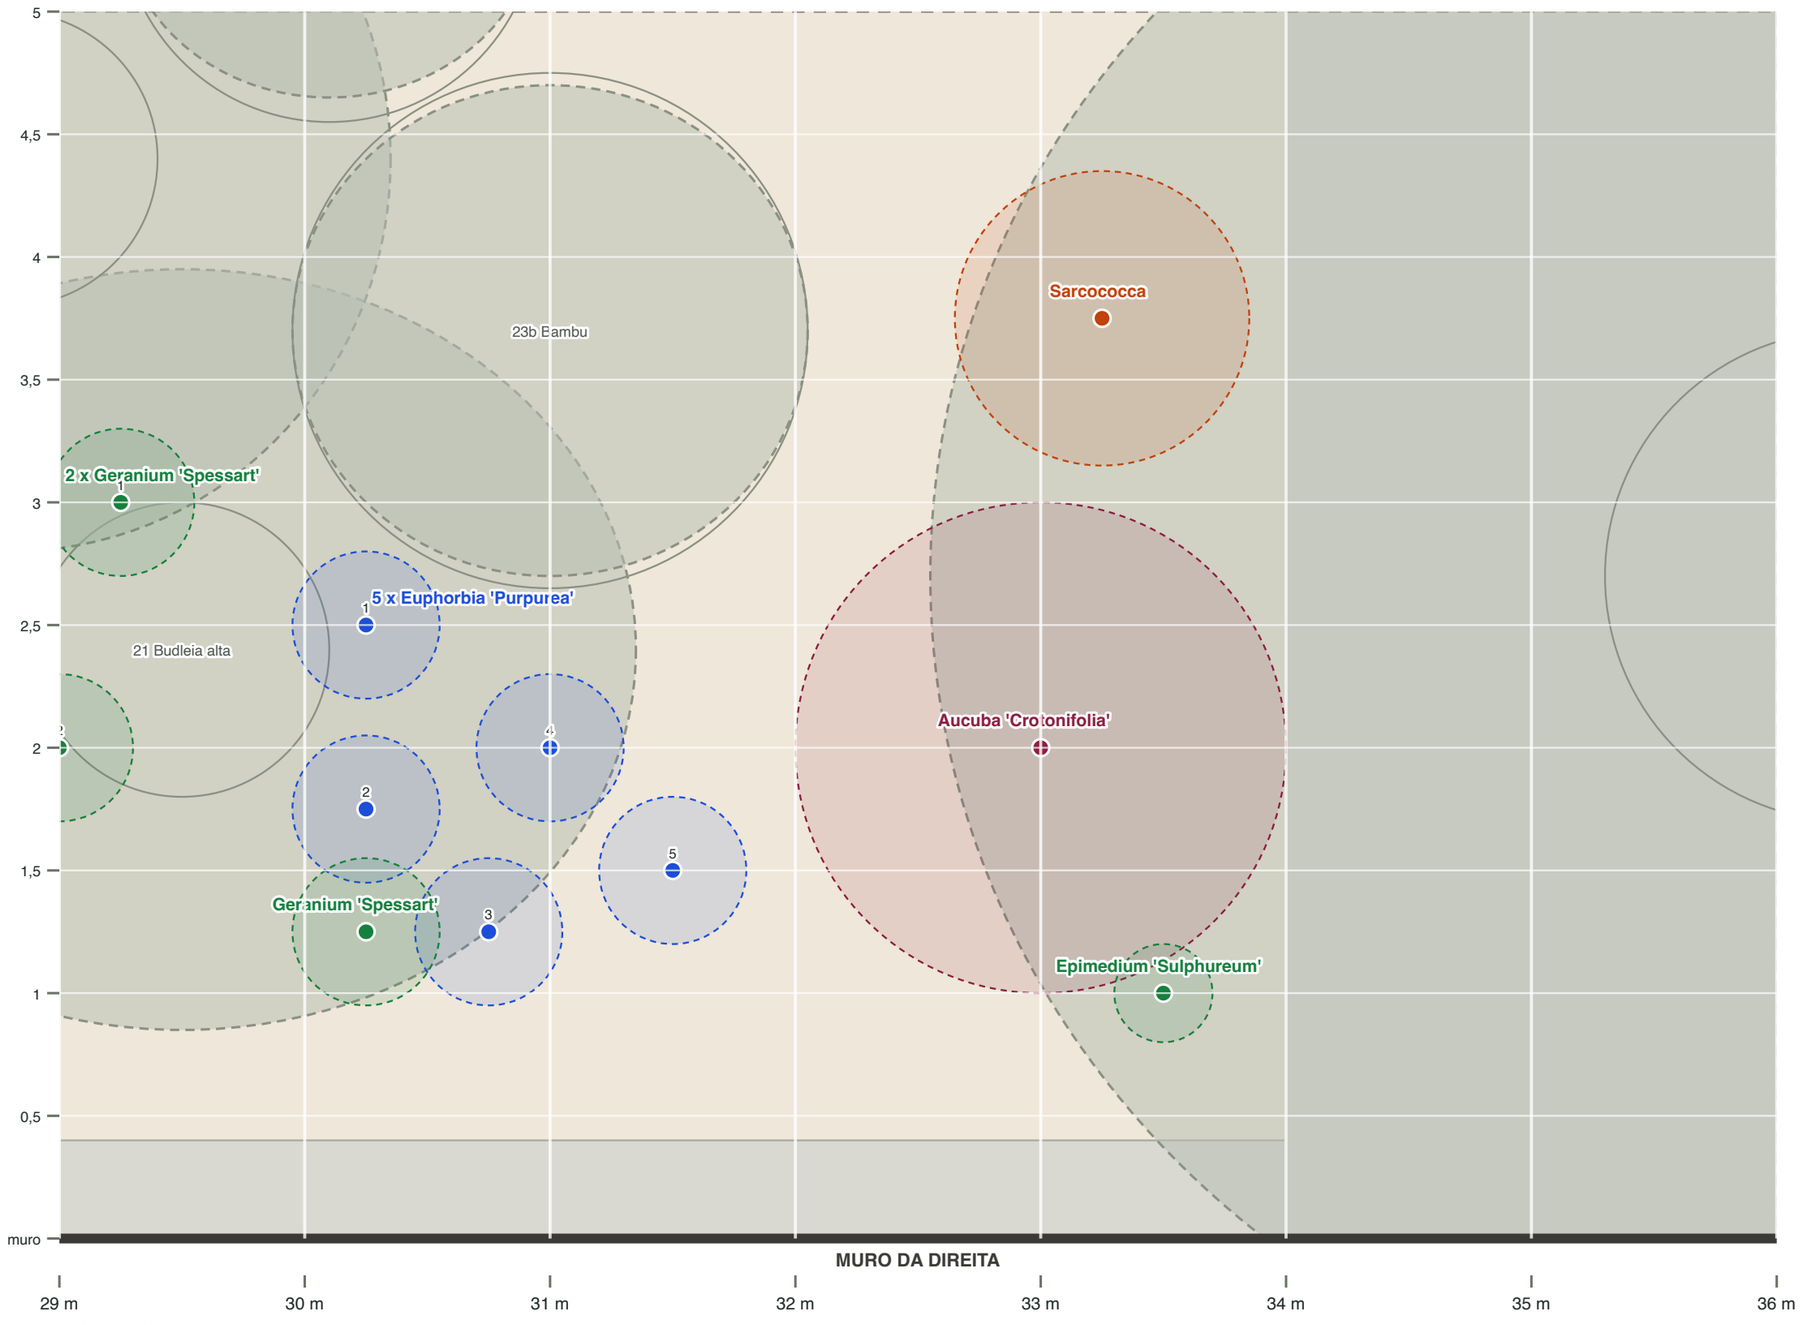

MARCAÇÃO: trena ao longo do muro, depois a partir do muro

2 x Geranium 'Spessart'	
1	29 ao longo, 2 do muro
2	29,25 ao longo, 3 do muro
5 x Euphorbia 'Purpurea'	
1	30,25 ao longo, 2,5 do muro
2	30,25 ao longo, 1,75 do muro
3	30,75 ao longo, 1,25 do muro
4	31 ao longo, 2 do muro
5	31,5 ao longo, 1,5 do muro
Geranium 'Spessart'	30,25 ao longo, 1,25 do muro
Aucuba 'Crotonifolia'	33 ao longo, 2 do muro
Sarcococca	33,25 ao longo, 3,75 do muro
Epimedium 'Sulphureum'	33,5 ao longo, 1 do muro


ANTES DE CAVAR

As posições vêm de um levantamento por fotos, não de uma medição.
Coloque todos os vasos no lugar, caminhe pelos canteiros e só então cave.


Bosque dos fundos e canteiros da casa

Escala 1:68. Casa embaixo em cada painel. O gramado e os canteiros entre 3,5 m e 31 m estão nas folhas 2 a 9.

BOSQUE DOS FUNDOS, os últimos 12 m antes do muro do fundo (31 a 43 m da casa)

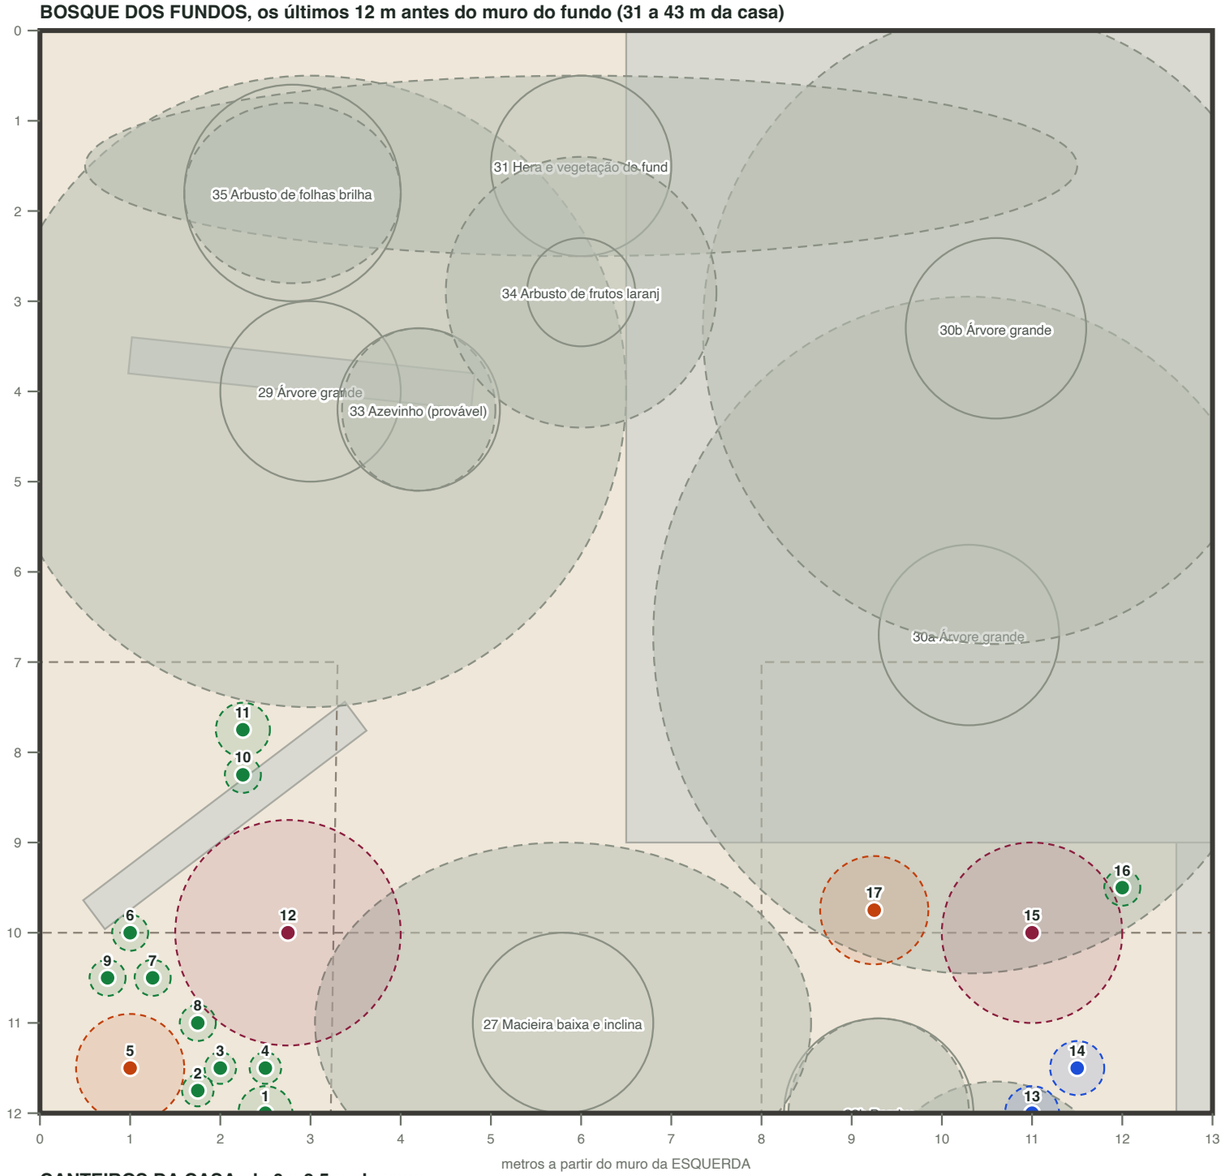

CANTEIROS DA CASA, de 0 a 3,5 m da casa

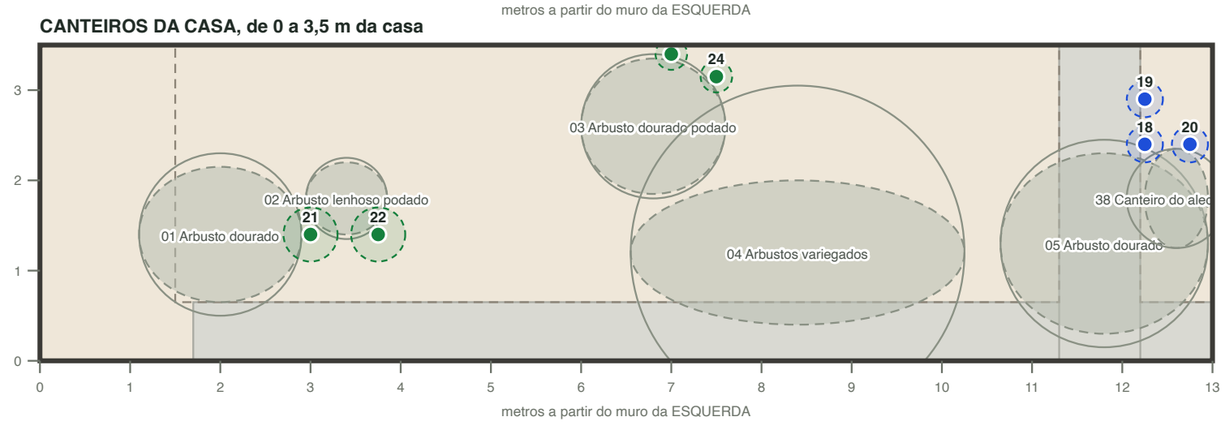

Gerado em 2026-11-05 a partir do levantamento fotográfico (rev. 04) e do pedido de 129 plantas da Palmstead.

MARCAÇÃO: fundo = do MURO DO FUNDO; casa = da casa; depois do muro da esquerda

1 Geranium 'Spessart'	12 do muro do fundo, 2,5 do muro da esquerda
2 Liriope	11,75 do muro do fundo, 1,75 do muro da esquerda
3 Liriope	11,5 do muro do fundo, 2 do muro da esquerda
4 Liriope	11,5 do muro do fundo, 2,5 do muro da esquerda
5 Sarcococca	11,5 do muro do fundo, 1 do muro da esquerda
6 Epimedium 'Sulphureum'	10 do muro do fundo, 1 do muro da esquerda
7 Epimedium 'Sulphureum'	10,5 do muro do fundo, 1,25 do muro da esquerda
8 Epimedium 'Sulphureum'	11 do muro do fundo, 1,75 do muro da esquerda
9 Epimedium 'Sulphureum'	10,5 do muro do fundo, 0,75 do muro da esquerda
10 Epimedium 'Sulphureum'	8,25 do muro do fundo, 2,25 do muro da esquerda
11 Geranium 'Spessart'	7,75 do muro do fundo, 2,25 do muro da esquerda
12 Osmanthus	10 do muro do fundo, 2,75 do muro da esquerda
13 Euphorbia 'Purpurea'	12 do muro do fundo, 11 do muro da esquerda
14 Euphorbia 'Purpurea'	11,5 do muro do fundo, 11,5 do muro da esquerda
15 Aucuba 'Crotonifolia'	10 do muro do fundo, 11 do muro da esquerda
16 Epimedium 'Sulphureum'	9,5 do muro do fundo, 12 do muro da esquerda
17 Sarcococca	9,75 do muro do fundo, 9,25 do muro da esquerda
18 Bergenia 'Bressingham White'	2,4 da casa, 12,25 do muro da esquerda
19 Bergenia 'Bressingham White'	2,9 da casa, 12,25 do muro da esquerda
20 Bergenia 'Bressingham White'	2,4 da casa, 12,75 do muro da esquerda
21 Geranium 'Spessart'	1,4 da casa, 3 do muro da esquerda
22 Geranium 'Spessart'	1,4 da casa, 3,75 do muro da esquerda
23 Liriope	3,4 da casa, 7 do muro da esquerda
24 Liriope	3,15 da casa, 7,5 do muro da esquerda

FUNDO À DIREITA, ATRÁS DO BAMBU

Há ali uma cerca viva e um caminho que não estão neste plano.
Mantenha o caminho livre. Plante só onde dá para cavar com a mão, entre as raízes.

ANTES DE CAVAR

As posições vêm de um levantamento por fotos, não de uma medição.
Coloque todos os vasos no lugar, caminhe pelos canteiros e só então cave.

Conferência e decisões pendentes

Confira a entrega com esta lista antes de marcar.

CONFERÊNCIA POR VARIEDADE

Planta	Pedido	No plano	Vaso
Anemone × hybrida 'Honorine Jobert'	3	3	2 L
Artemisia 'Powis Castle'	3	3	2 L
Aucuba japonica 'Crotonifolia'	2	2	10 L
Bergenia 'Bressingham White'	5	5	2 L
Calamagrostis brachytricha	5	5	2 L
Chaenomeles × superba 'Crimson & Gold'	2	2	2 L
Choisya ternata	1	1	7,5 L
Cotinus coggygria 'Royal Purple'	1	1	25 L
Deutzia gracilis 'Nikko'	9	9	2 L
Epimedium × versicolor 'Sulphureum'	16	16	2 L
Euphorbia amygdaloides 'Purpurea'	5	5	2 L
Geranium 'Rozanne'	6	6	2 L
Geranium macrorrhizum 'Spessart'	37	37	2 L
Liriope muscari	5	5	2 L
Nepeta racemosa 'Walker's Low'	6	6	2 L
Osmanthus × burkwoodii	1	1	5 L
Philadelphus 'Virginal'	1	1	25 L
Salvia nemorosa 'Caradonna'	5	5	2 L
Sarcococca confusa	3	3	4 L
Skimmia japonica 'Rubella'	3	3	2 L
Polystichum setiferum	5	5	2 L
Spiraea japonica 'Goldflame'	3	3	1,5 L
Viburnum × bodnantense 'Dawn'	1	1	10 L
Viburnum tinus 'Eve Price'	1	1	2 L
Total	**129**	**129**	

VASOS POR CANTEIRO

canteiro da esquerda	73
canteiro da direita	45
bosque dos fundos	4
canteiro da casa, à esquerda da escada	4
canteiro do alecrim, junto à escada	3

DECISÕES PENDENTES (em inglês, para o proprietário)

G04-3 Skimmia 'Rubella' moved 15.38 m along the bed to find part-or-shade; confirm or override.

K01-1 Aucuba 'Crotonifolia' at (11, 33) is in the pocket behind the bamboo; the hedge and the path there are not on the survey, keep the path clear.

K02-1 Epimedium 'Sulphureum' at (12, 33.5) is in the pocket behind the bamboo; the hedge and the path there are not on the survey, keep the path clear.

K04-1 Sarcococca at (9.25, 33.25) is in the pocket behind the bamboo; the hedge and the path there are not on the survey, keep the path clear.

O QUE O PLANO PRESSUPÕE

O jardim tem 43 por 13 m, segundo a planta da imobiliária, não medido.
As bordas dos canteiros, o caminho e cada planta existente vêm de um levantamento por fotos (revisão 04, 24 de outubro de 2026).
O canteiro do alecrim e sua escada ficam na ponta direita da frente da casa, olhando para fora.
Os arbustos foram planejados no tamanho podado e podem avançar sobre o gramado, mas não sobre o caminho.
Plantas de sol só vão onde nada as sombreia; plantas de sombra nunca vão para o sol pleno.
Cada planta do pedido da Palmstead está no plano uma vez. Não há substituições.

TRÊS COISAS DE QUE O PLANO DEPENDE

1. Pode a budleia junto ao terraço (17) e a budleia alta (21) até uns 60 cm todo mês de março, senão as plantas na frente delas vão ficar embaixo.

2. Mantenha o eleagno prateado grande (07) aparado na linha atual do lado do caminho; as Artemisia ao lado precisam de sol.

3. Teste o solo com um kit de pH antes de plantar as Skimmia e as Liriope. Se der acima de 7, plante em substrato para plantas acidófilas.

ANTES DE CAVAR

As posições vêm de um levantamento por fotos, não de uma medição.
Coloque todos os vasos no lugar, caminhe pelos canteiros e só então cave.