
# Jardim inteiro, casa embaixo

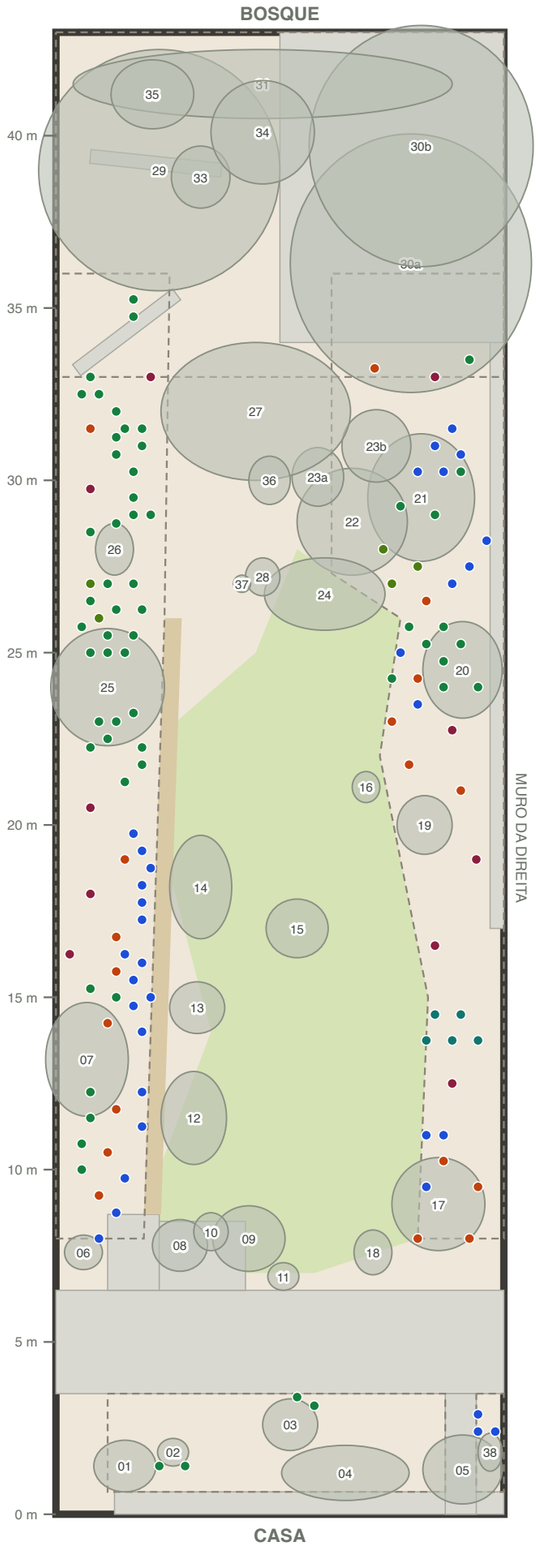

Escala 1:178. Esquerda e direita como vistas da casa olhando para o bosque. Formas cinza são plantas existentes. Pontos coloridos são os 129 vasos novos.




Fundo e canteiros da casa: folha 10

Esquerda: folha 5; direita: folha 9

Esquerda: folha 4; direita: folha 8

Esquerda: folha 3; direita: folha 7

Esquerda: folha 2; direita: folha 6

## PLANTAS NOVAS POR TIPO

- Arbusto estrutural: 10 vasos
- Arbusto de flor: 18 vasos
- Perene: 33 vasos
- Gramínea: 5 vasos
- Forração: 58 vasos
- Samambaia: 5 vasos

## PLANTAS E ELEMENTOS EXISTENTES (cinza, numerados como no levantamento)

| | |
|---|---|
| **29** | Árvore grande, fundo esquerdo |
| **30a** | Árvore grande, fundo direito A |
| **30b** | Árvore grande, fundo direito B |
| **31** | Hera e vegetação do fundo |
| **01** | Arbusto dourado, canteiro baixo |
| **02** | Arbusto lenhoso podado |
| **03** | Arbusto dourado podado |
| **04** | Arbustos variegados, canteiro baixo |
| **05** | Arbusto dourado, direita baixa |
| **06** | Arbusto pequeno junto ao muro esquerdo |
| **07** | Eleagno grande |
| **08** | Euonymus dourado, floreira esquerda |
| **09** | Euonymus dourado, floreira direita |
| **10** | Grupo misto na floreira |
| **11** | Touceira de folhas longas |
| **12** | Acanto e folhas longas |
| **13** | Acanto, meio |
| **14** | Touceira de folhas longas, mais ao fundo |
| **15** | Acanto central |
| **16** | Arbusto pequeno no gramado |
| **17** | Budleia junto ao terraço |
| **18** | Arbusto pequeno junto ao terraço |
| **19** | Hipérico (provável) |
| **20** | Arvoreta junto ao muro direito |
| **21** | Budleia alta |
| **22** | Fátsia |
| **23a** | Bambu, touceira clara |
| **23b** | Bambu, touceira escura |
| **24** | Acantos abaixo da fátsia |
| **25** | Macieira (provável) |
| **26** | Arbusto podado, esquerda |
| **27** | Macieira baixa e inclinada |
| **28** | Touceira pequena podada |
| **33** | Azevinho (provável) |
| **34** | Arbusto de frutos laranja |
| **35** | Arbusto de folhas brilhantes |
| **36** | Fátsia jovem |
| **37** | Toco cortado |
| **38** | Canteiro do alecrim junto à escada |

## Como usar este plano

1. Encontre o trecho do canteiro nesta página e vá até a folha dele.
2. Prenda a trena na ponta do muro junto à casa e leia o primeiro número ao longo dele.
3. Estique uma segunda trena em linha reta a partir do muro e leia o segundo número.
4. Coloque o vaso no lugar. Marque o trecho inteiro antes de cavar qualquer coisa.
5. Se um vaso cair sobre uma raiz, deslize-o ao longo do canteiro, não em direção ao caminho ou ao gramado.

**ANTES DE CAVAR**

As posições vêm de um levantamento por fotos, não de uma medição.
Coloque todos os vasos no lugar, caminhe pelos canteiros e só então cave.

Gerado em 2026-11-05 a partir do levantamento fotográfico (rev. 04) e do pedido de 129 plantas da Palmstead.


# Canteiro da esquerda, de 8 a 15 m da casa



A casa fica à ESQUERDA desta folha e o bosque à DIREITA. O MURO DA ESQUERDA corre pela parte de CIMA. Escala 1:25. Ponto = centro do vaso. Círculo claro = espaço de que a planta precisa.

< PARA A CASA

PARA O BOSQUE >

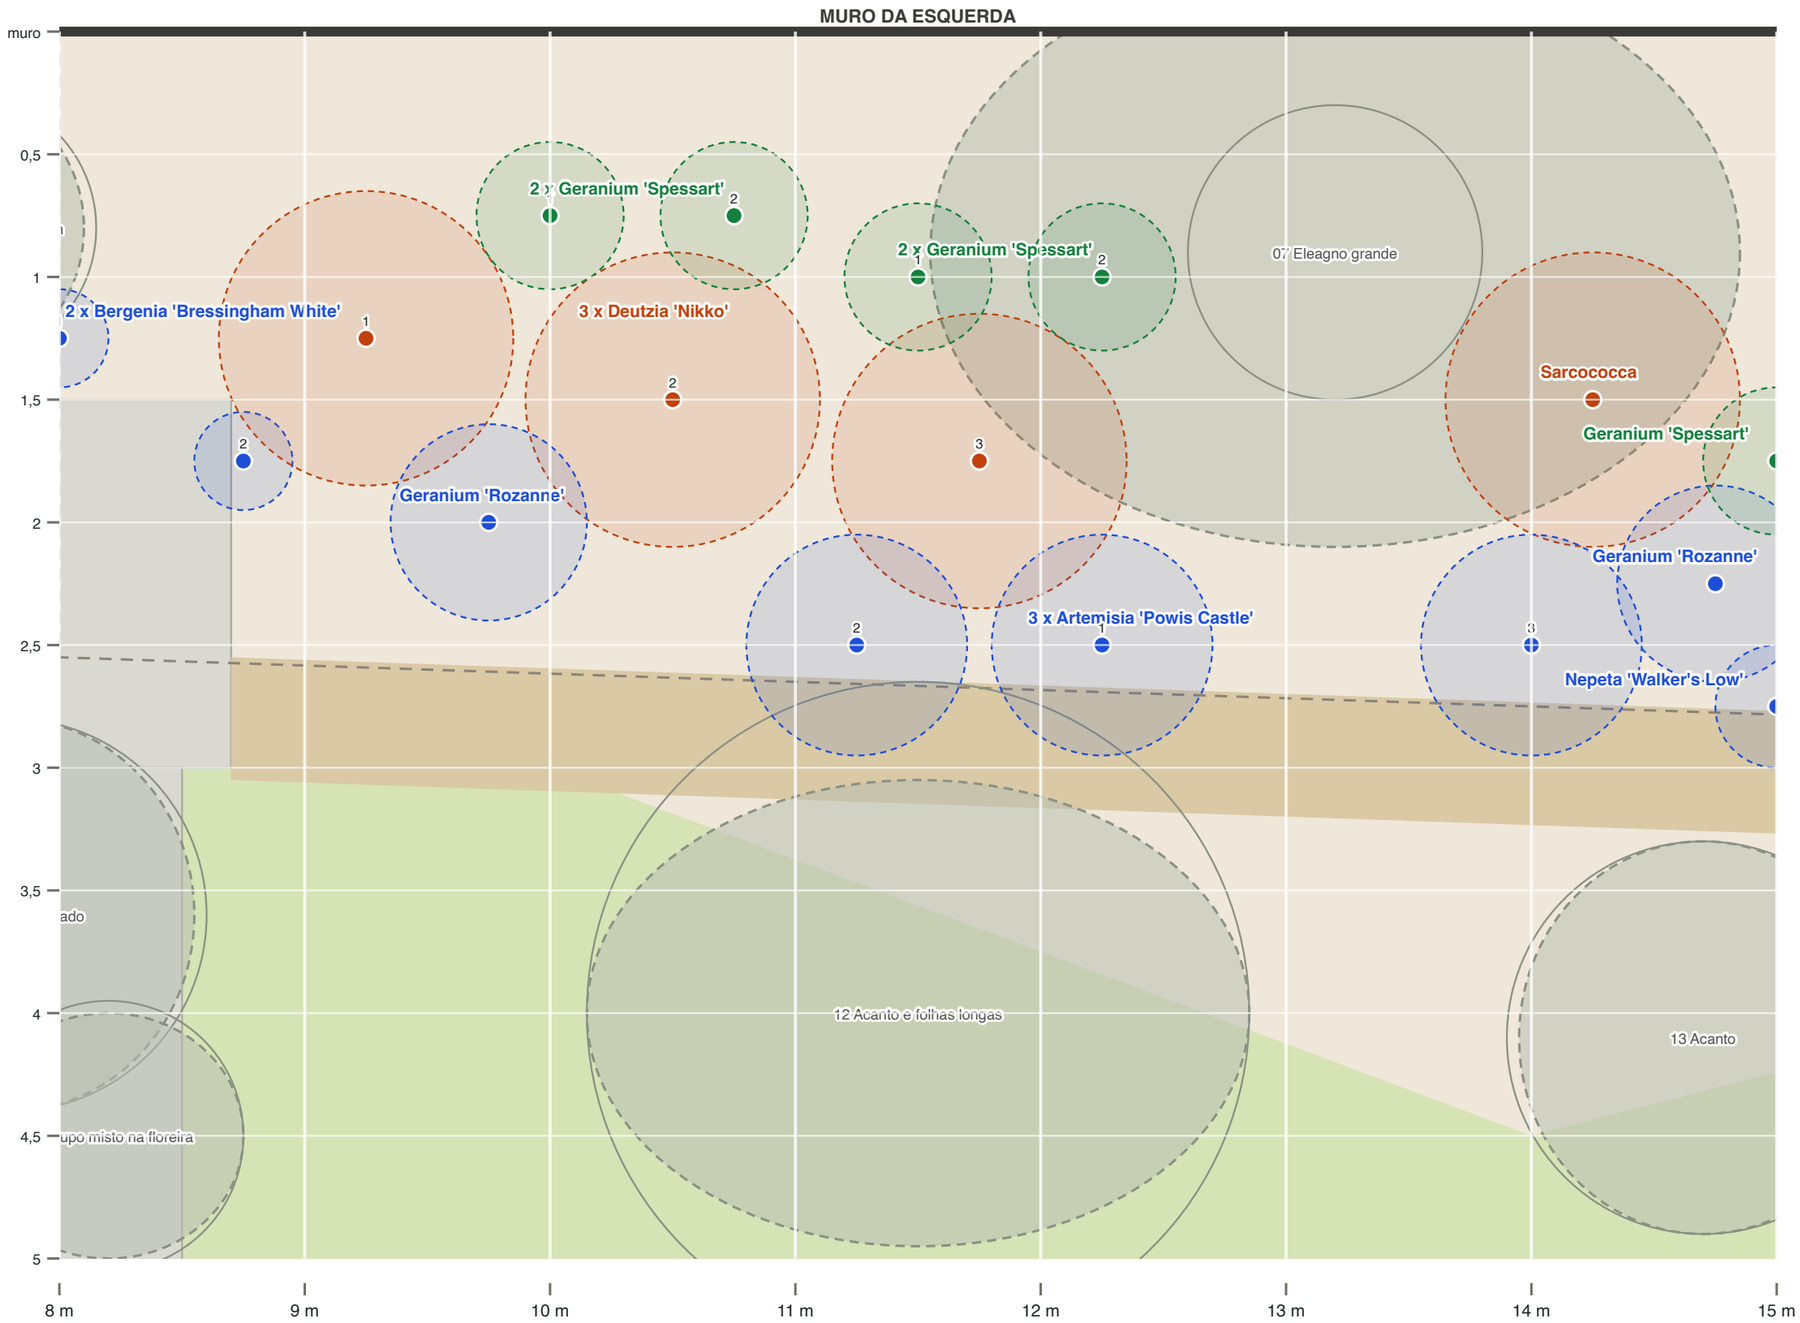


**MARCAÇÃO: trena ao longo do muro, depois a partir do muro**

| | |
|---|---|
| **2 x Bergenia 'Bressingham White'** | |
| 1 | 8 ao longo, 1,25 do muro |
| 2 | 8,75 ao longo, 1,75 do muro |
| **3 x Deutzia 'Nikko'** | |
| 1 | 9,25 ao longo, 1,25 do muro |
| 2 | 10,5 ao longo, 1,5 do muro |
| 3 | 11,75 ao longo, 1,75 do muro |
| **Geranium 'Rozanne'** | 9,75 ao longo, 2 do muro |
| **2 x Geranium 'Spessart'** | |
| 1 | 10 ao longo, 0,75 do muro |
| 2 | 10,75 ao longo, 0,75 do muro |
| **3 x Artemisia 'Powis Castle'** | |
| 1 | 11,25 ao longo, 2,5 do muro |
| 2 | 12,25 ao longo, 2,5 do muro |
| 3 | 14 ao longo, 2,5 do muro |
| **2 x Geranium 'Spessart'** | |
| 1 | 11,5 ao longo, 1 do muro |
| 2 | 12,25 ao longo, 1 do muro |
| **Sarcococca** | 14,25 ao longo, 1,5 do muro |
| **Geranium 'Rozanne'** | 14,75 ao longo, 2,25 do muro |
| **Geranium 'Spessart'** | 15 ao longo, 1,75 do muro |
| **Nepeta 'Walker's Low'** | 15 ao longo, 2,75 do muro |

**ANTES DE CAVAR**

As posições vêm de um levantamento por fotos, não de uma medição.
Coloque todos os vasos no lugar, caminhe pelos canteiros e só então cave.


# Canteiro da esquerda, de 15 a 22 m da casa



A casa fica à ESQUERDA desta folha e o bosque à DIREITA. O MURO DA ESQUERDA corre pela parte de CIMA. Escala 1:25. Ponto = centro do vaso. Círculo claro = espaço de que a planta precisa.

< PARA A CASA

PARA O BOSQUE >

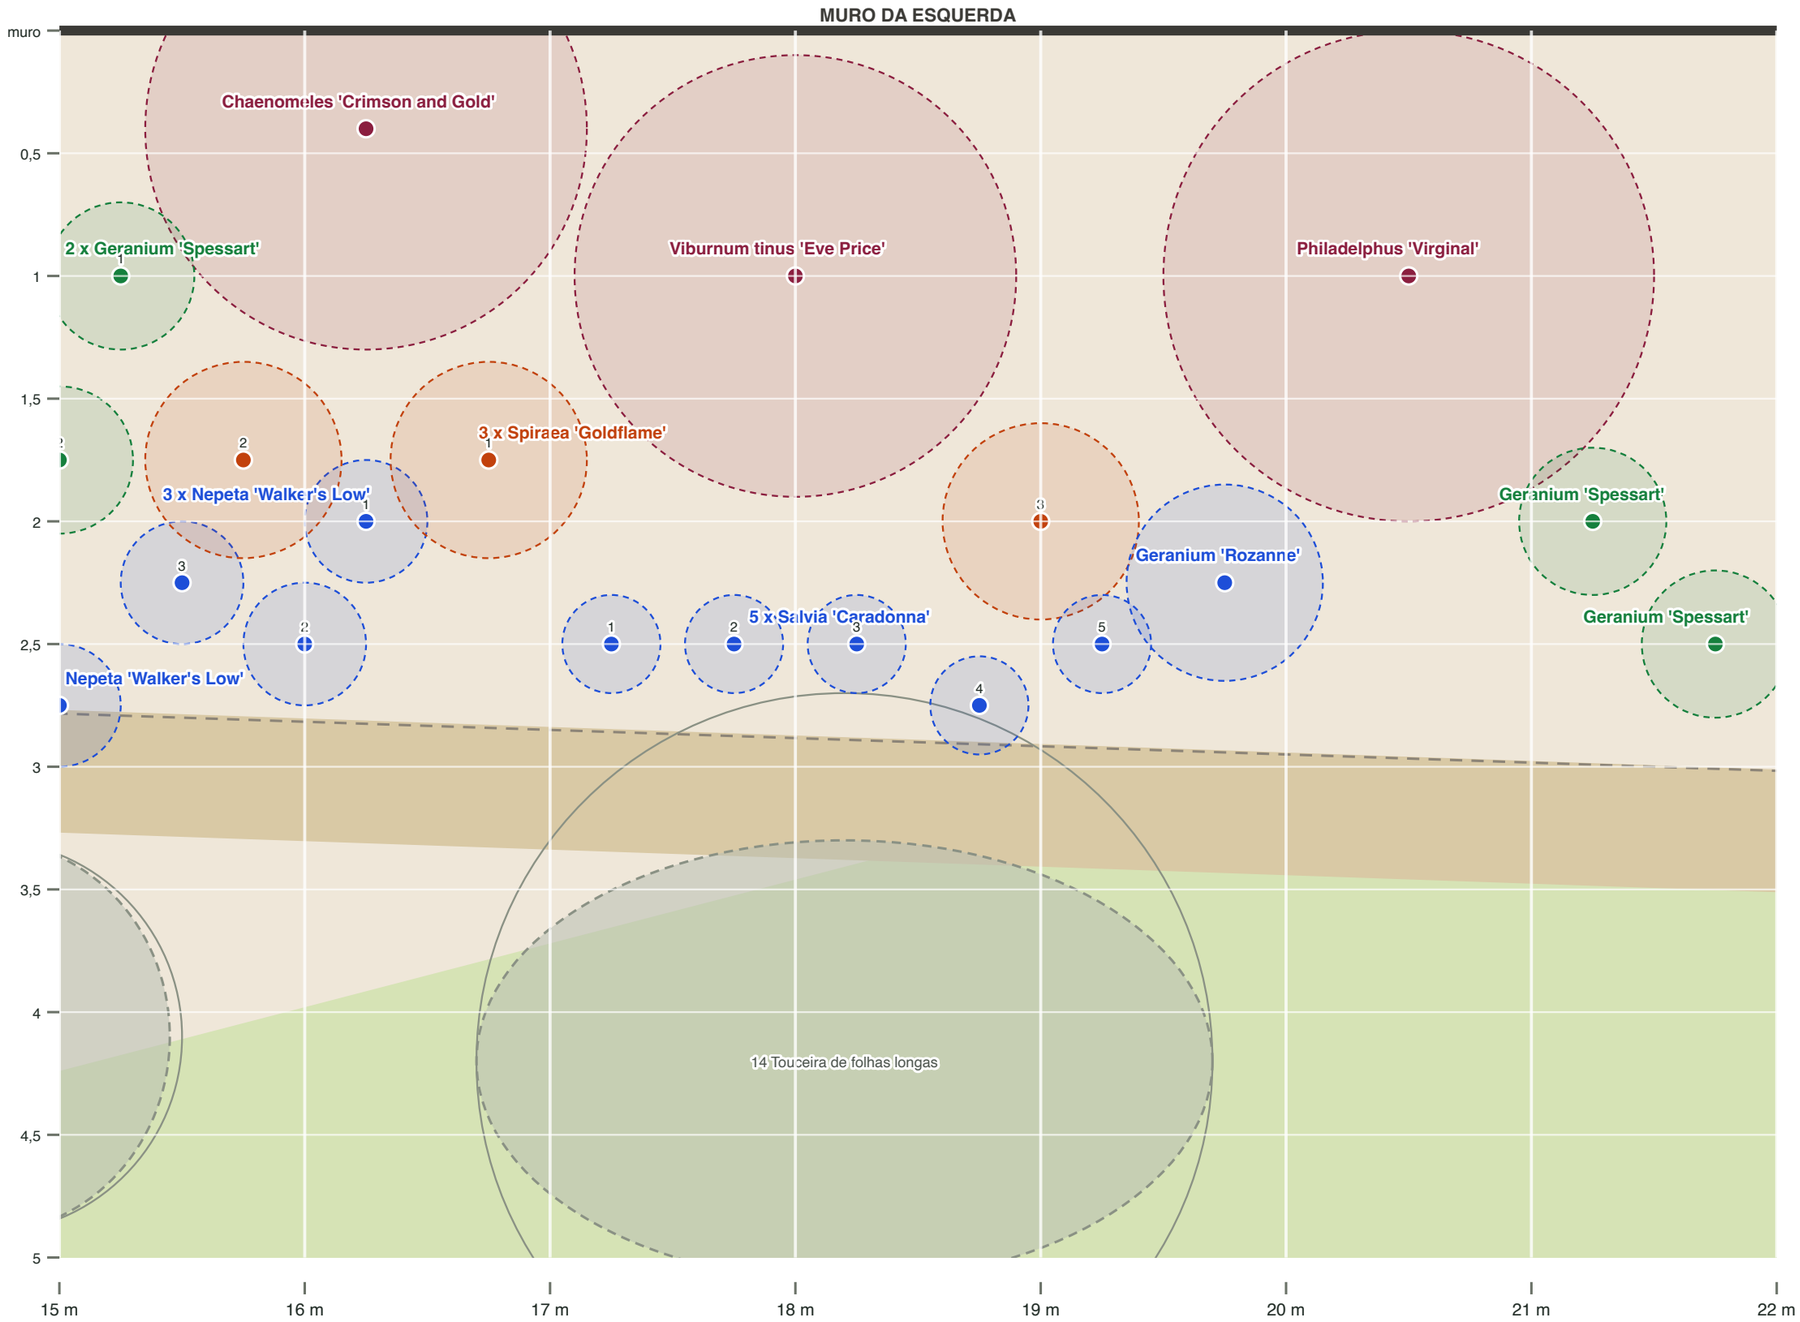


**MARCAÇÃO: trena ao longo do muro, depois a partir do muro**

| | |
|---|---|
| **2 x Geranium 'Spessart'** | |
| 1 | 15 ao longo, 1,75 do muro |
| 2 | 15,25 ao longo, 1 do muro |
| **Nepeta 'Walker's Low'** | 15 ao longo, 2,75 do muro |
| **3 x Nepeta 'Walker's Low'** | |
| 1 | 15,5 ao longo, 2,25 do muro |
| 2 | 16 ao longo, 2,5 do muro |
| 3 | 16,25 ao longo, 2 do muro |
| **3 x Spiraea 'Goldflame'** | |
| 1 | 15,75 ao longo, 1,75 do muro |
| 2 | 16,75 ao longo, 1,75 do muro |
| 3 | 19 ao longo, 2 do muro |
| **Chaenomeles 'Crimson and Gold'** | 16,25 ao longo, 0,4 do muro |
| **5 x Salvia 'Caradonna'** | |
| 1 | 17,25 ao longo, 2,5 do muro |
| 2 | 17,75 ao longo, 2,5 do muro |
| 3 | 18,25 ao longo, 2,5 do muro |
| 4 | 18,75 ao longo, 2,75 do muro |
| 5 | 19,25 ao longo, 2,5 do muro |
| **Viburnum tinus 'Eve Price'** | 18 ao longo, 1 do muro |
| **Geranium 'Rozanne'** | 19,75 ao longo, 2,25 do muro |
| **Philadelphus 'Virginal'** | 20,5 ao longo, 1 do muro |
| **Geranium 'Spessart'** | 21,25 ao longo, 2 do muro |
| **Geranium 'Spessart'** | 21,75 ao longo, 2,5 do muro |

**ANTES DE CAVAR**

As posições vêm de um levantamento por fotos, não de uma medição.
Coloque todos os vasos no lugar, caminhe pelos canteiros e só então cave.


# Canteiro da esquerda, de 22 a 29 m da casa



A casa fica à ESQUERDA desta folha e o bosque à DIREITA. O MURO DA ESQUERDA corre pela parte de CIMA. Escala 1:25. Ponto = centro do vaso. Círculo claro = espaço de que a planta precisa.

< PARA A CASA

PARA O BOSQUE >

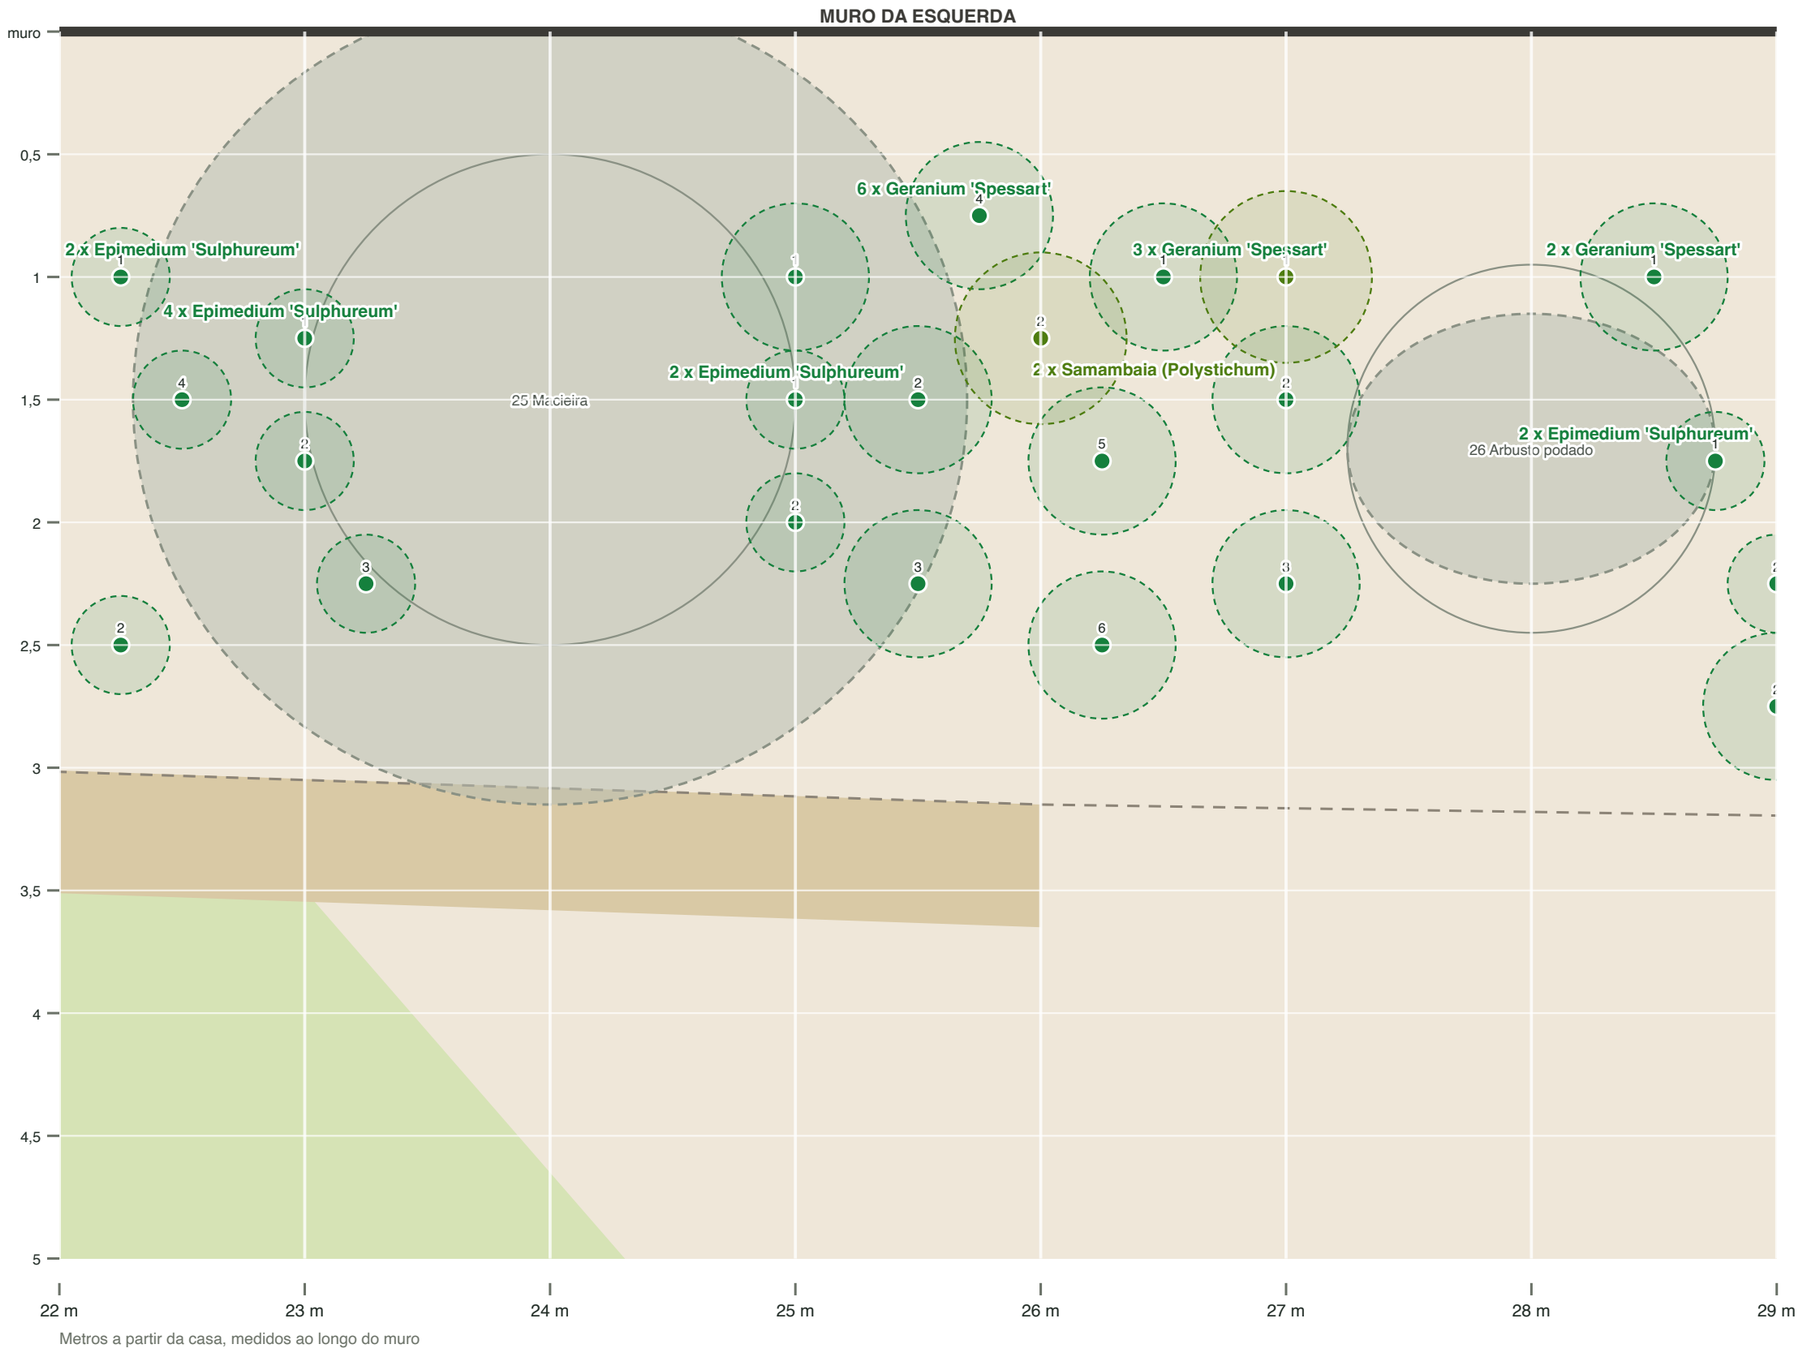


**MARCAÇÃO: trena ao longo do muro, depois a partir do muro**

- **2 x Epimedium 'Sulphureum'**
  - 1 — 22,25 ao longo, 1 do muro
  - 2 — 22,25 ao longo, 2,5 do muro
- **4 x Epimedium 'Sulphureum'**
  - 1 — 22,5 ao longo, 1,5 do muro
  - 2 — 23 ao longo, 1,25 do muro
  - 3 — 23 ao longo, 1,75 do muro
  - 4 — 23,25 ao longo, 2,25 do muro
- **6 x Geranium 'Spessart'**
  - 1 — 25 ao longo, 1 do muro
  - 2 — 25,5 ao longo, 1,5 do muro
  - 3 — 25,5 ao longo, 2,25 do muro
  - 4 — 25,75 ao longo, 0,75 do muro
  - 5 — 26,25 ao longo, 1,75 do muro
  - 6 — 26,25 ao longo, 2,5 do muro
- **2 x Epimedium 'Sulphureum'**
  - 1 — 25 ao longo, 1,5 do muro
  - 2 — 25 ao longo, 2 do muro
- **2 x Samambaia (Polystichum)**
  - 1 — 26 ao longo, 1,25 do muro
  - 2 — 27 ao longo, 1 do muro
- **3 x Geranium 'Spessart'**
  - 1 — 26,5 ao longo, 1 do muro
  - 2 — 27 ao longo, 1,5 do muro
  - 3 — 27 ao longo, 2,25 do muro
- **2 x Geranium 'Spessart'**
  - 1 — 28,5 ao longo, 1 do muro
  - 2 — 29 ao longo, 2,75 do muro
- **2 x Epimedium 'Sulphureum'**
  - 1 — 28,75 ao longo, 1,75 do muro
  - 2 — 29 ao longo, 2,25 do muro

**ANTES DE CAVAR**

As posições vêm de um levantamento por fotos, não de uma medição.
Coloque todos os vasos no lugar, caminhe pelos canteiros e só então cave.


# Canteiro da esquerda, de 29 a 36 m da casa



A casa fica à ESQUERDA desta folha e o bosque à DIREITA. O MURO DA ESQUERDA corre pela parte de CIMA. Escala 1:25. Ponto = centro do vaso. Círculo claro = espaço de que a planta precisa.

< PARA A CASA

PARA O BOSQUE >

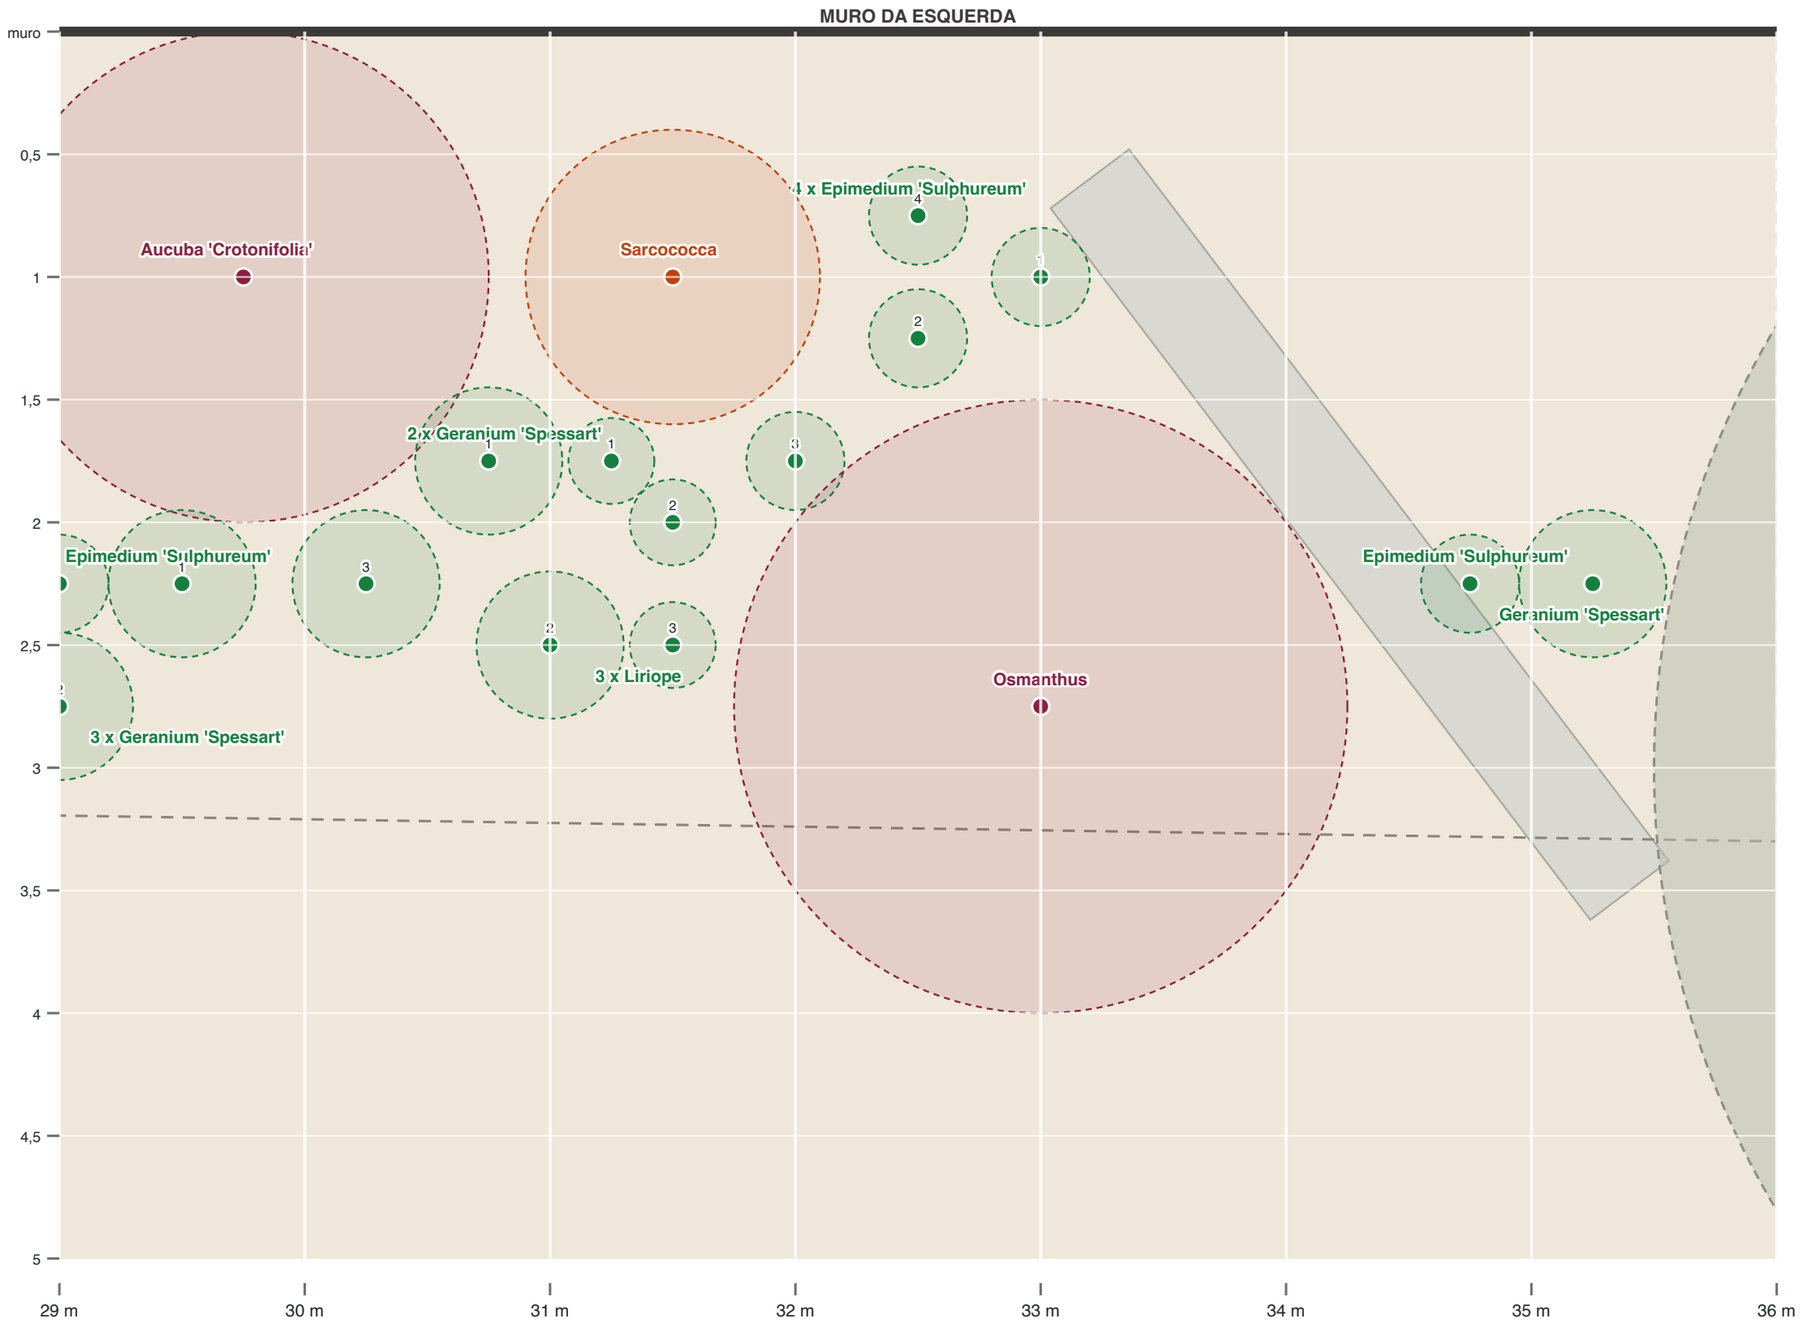


**MARCAÇÃO: trena ao longo do muro, depois a partir do muro**

| | |
|---|---|
| **Epimedium 'Sulphureum'** | 29 ao longo, 2,25 do muro |
| **3 x Geranium 'Spessart'** | |
| 1 | 29 ao longo, 2,75 do muro |
| 2 | 29,5 ao longo, 2,25 do muro |
| 3 | 30,25 ao longo, 2,25 do muro |
| **Aucuba 'Crotonifolia'** | 29,75 ao longo, 1 do muro |
| **2 x Geranium 'Spessart'** | |
| 1 | 30,75 ao longo, 1,75 do muro |
| 2 | 31 ao longo, 2,5 do muro |
| **3 x Liriope** | |
| 1 | 31,25 ao longo, 1,75 do muro |
| 2 | 31,5 ao longo, 2 do muro |
| 3 | 31,5 ao longo, 2,5 do muro |
| **Sarcococca** | 31,5 ao longo, 1 do muro |
| **4 x Epimedium 'Sulphureum'** | |
| 1 | 32 ao longo, 1,75 do muro |
| 2 | 32,5 ao longo, 0,75 do muro |
| 3 | 32,5 ao longo, 1,25 do muro |
| 4 | 33 ao longo, 1 do muro |
| **Osmanthus** | 33 ao longo, 2,75 do muro |
| **Epimedium 'Sulphureum'** | 34,75 ao longo, 2,25 do muro |
| **Geranium 'Spessart'** | 35,25 ao longo, 2,25 do muro |

**ANTES DE CAVAR**

As posições vêm de um levantamento por fotos, não de uma medição.
Coloque todos os vasos no lugar, caminhe pelos canteiros e só então cave.


# Canteiro da direita, de 8 a 15 m da casa



A casa fica à ESQUERDA desta folha e o bosque à DIREITA. O MURO DA DIREITA corre pela parte de BAIXO. Escala 1:25. Ponto = centro do vaso. Círculo claro = espaço de que a planta precisa.

< PARA A CASA

PARA O BOSQUE >

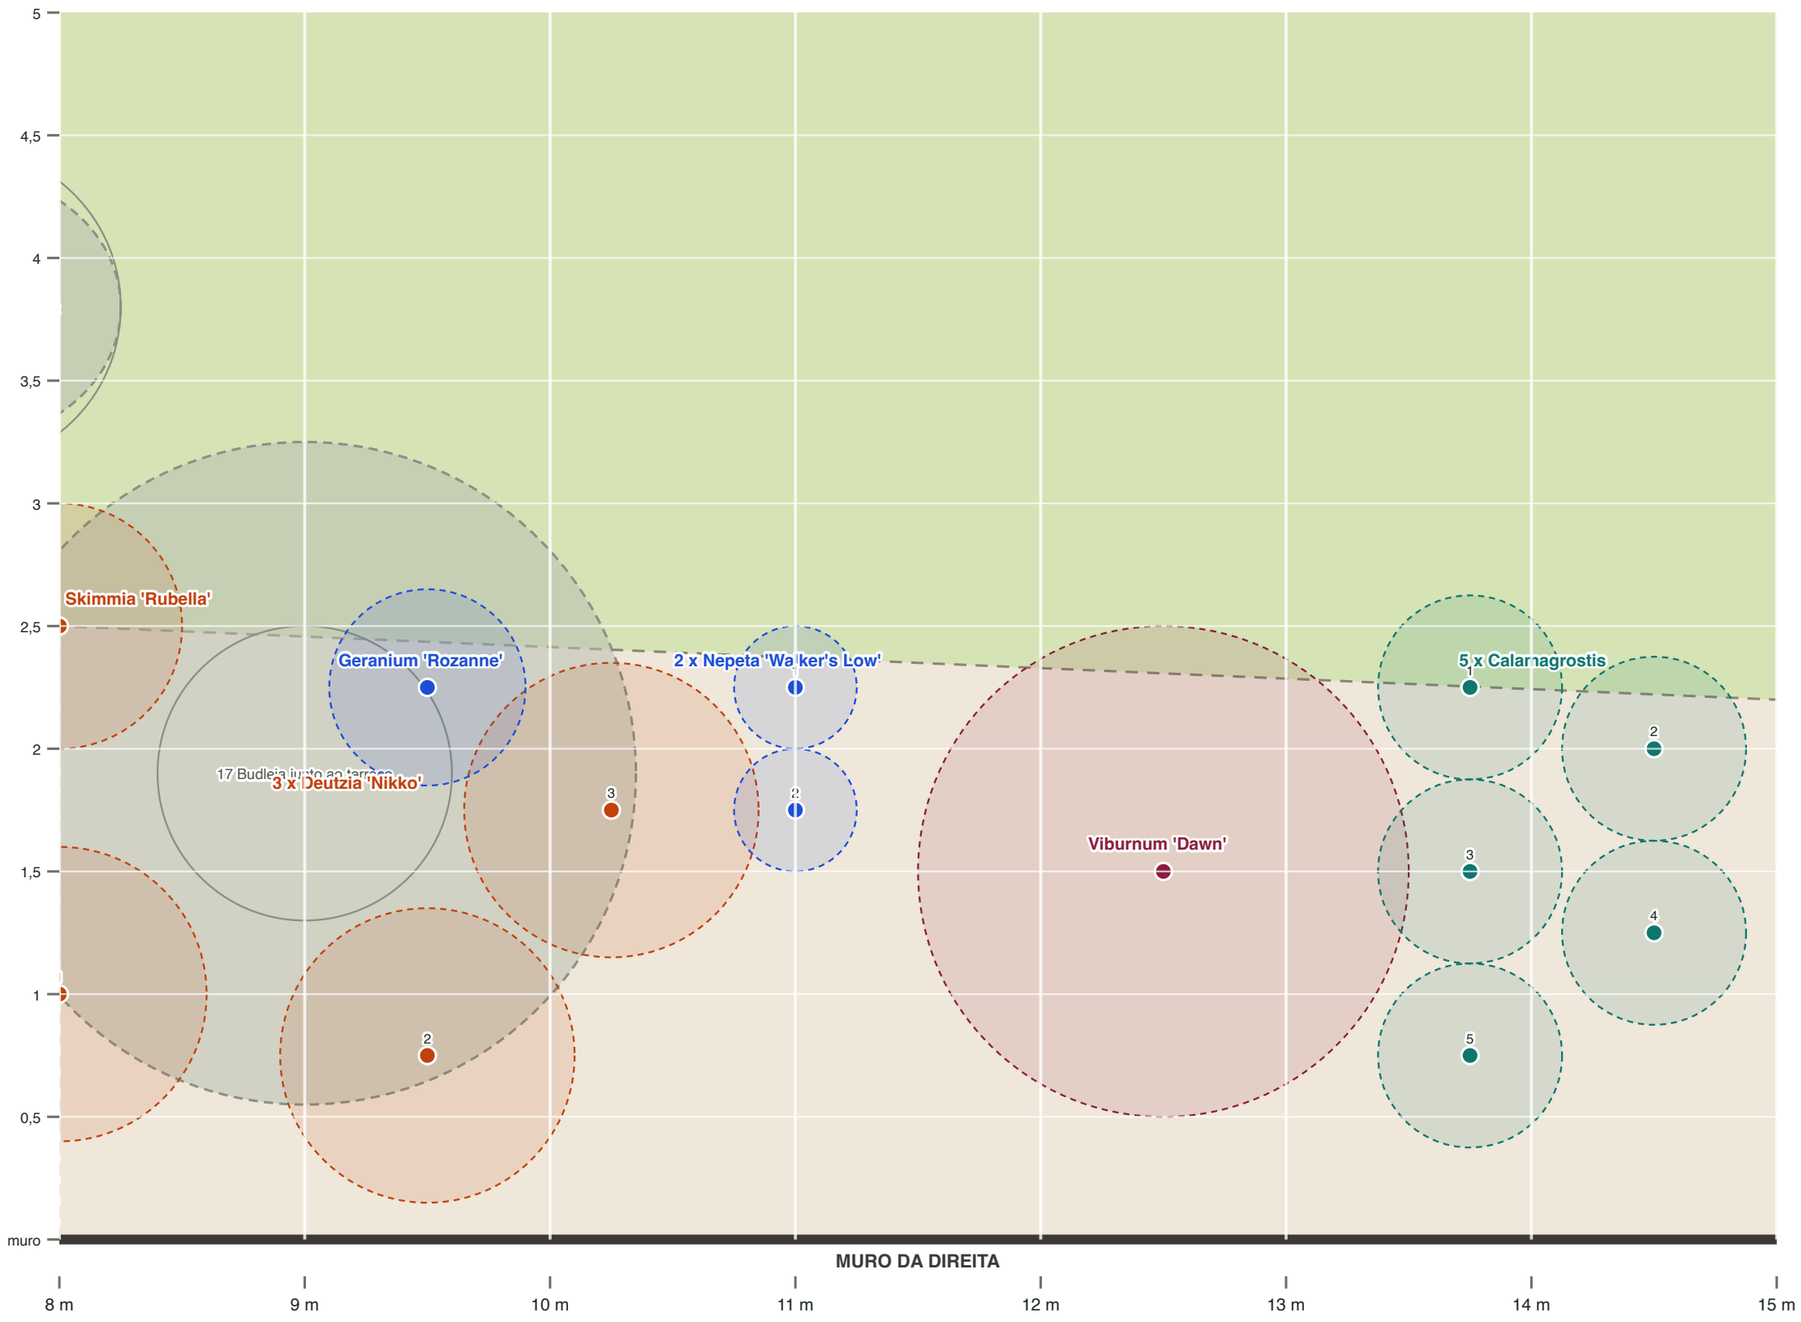


**MARCAÇÃO: trena ao longo do muro, depois a partir do muro**

| | |
|---|---|
| **Skimmia 'Rubella'** | 8 ao longo, 2,5 do muro |
| **3 x Deutzia 'Nikko'** | |
| 1 | 8 ao longo, 1 do muro |
| 2 | 9,5 ao longo, 0,75 do muro |
| 3 | 10,25 ao longo, 1,75 do muro |
| **Geranium 'Rozanne'** | 9,5 ao longo, 2,25 do muro |
| **2 x Nepeta 'Walker's Low'** | |
| 1 | 11 ao longo, 2,25 do muro |
| 2 | 11 ao longo, 1,75 do muro |
| **Viburnum 'Dawn'** | 12,5 ao longo, 1,5 do muro |
| **5 x Calamagrostis** | |
| 1 | 13,75 ao longo, 2,25 do muro |
| 2 | 13,75 ao longo, 1,5 do muro |
| 3 | 13,75 ao longo, 0,75 do muro |
| 4 | 14,5 ao longo, 2 do muro |
| 5 | 14,5 ao longo, 1,25 do muro |

**ANTES DE CAVAR**

As posições vêm de um levantamento por fotos, não de uma medição.
Coloque todos os vasos no lugar, caminhe pelos canteiros e só então cave.


# Canteiro da direita, de 15 a 22 m da casa



A casa fica à ESQUERDA desta folha e o bosque à DIREITA. O MURO DA DIREITA corre pela parte de BAIXO. Escala 1:25. Ponto = centro do vaso. Círculo claro = espaço de que a planta precisa.

< PARA A CASA

PARA O BOSQUE >

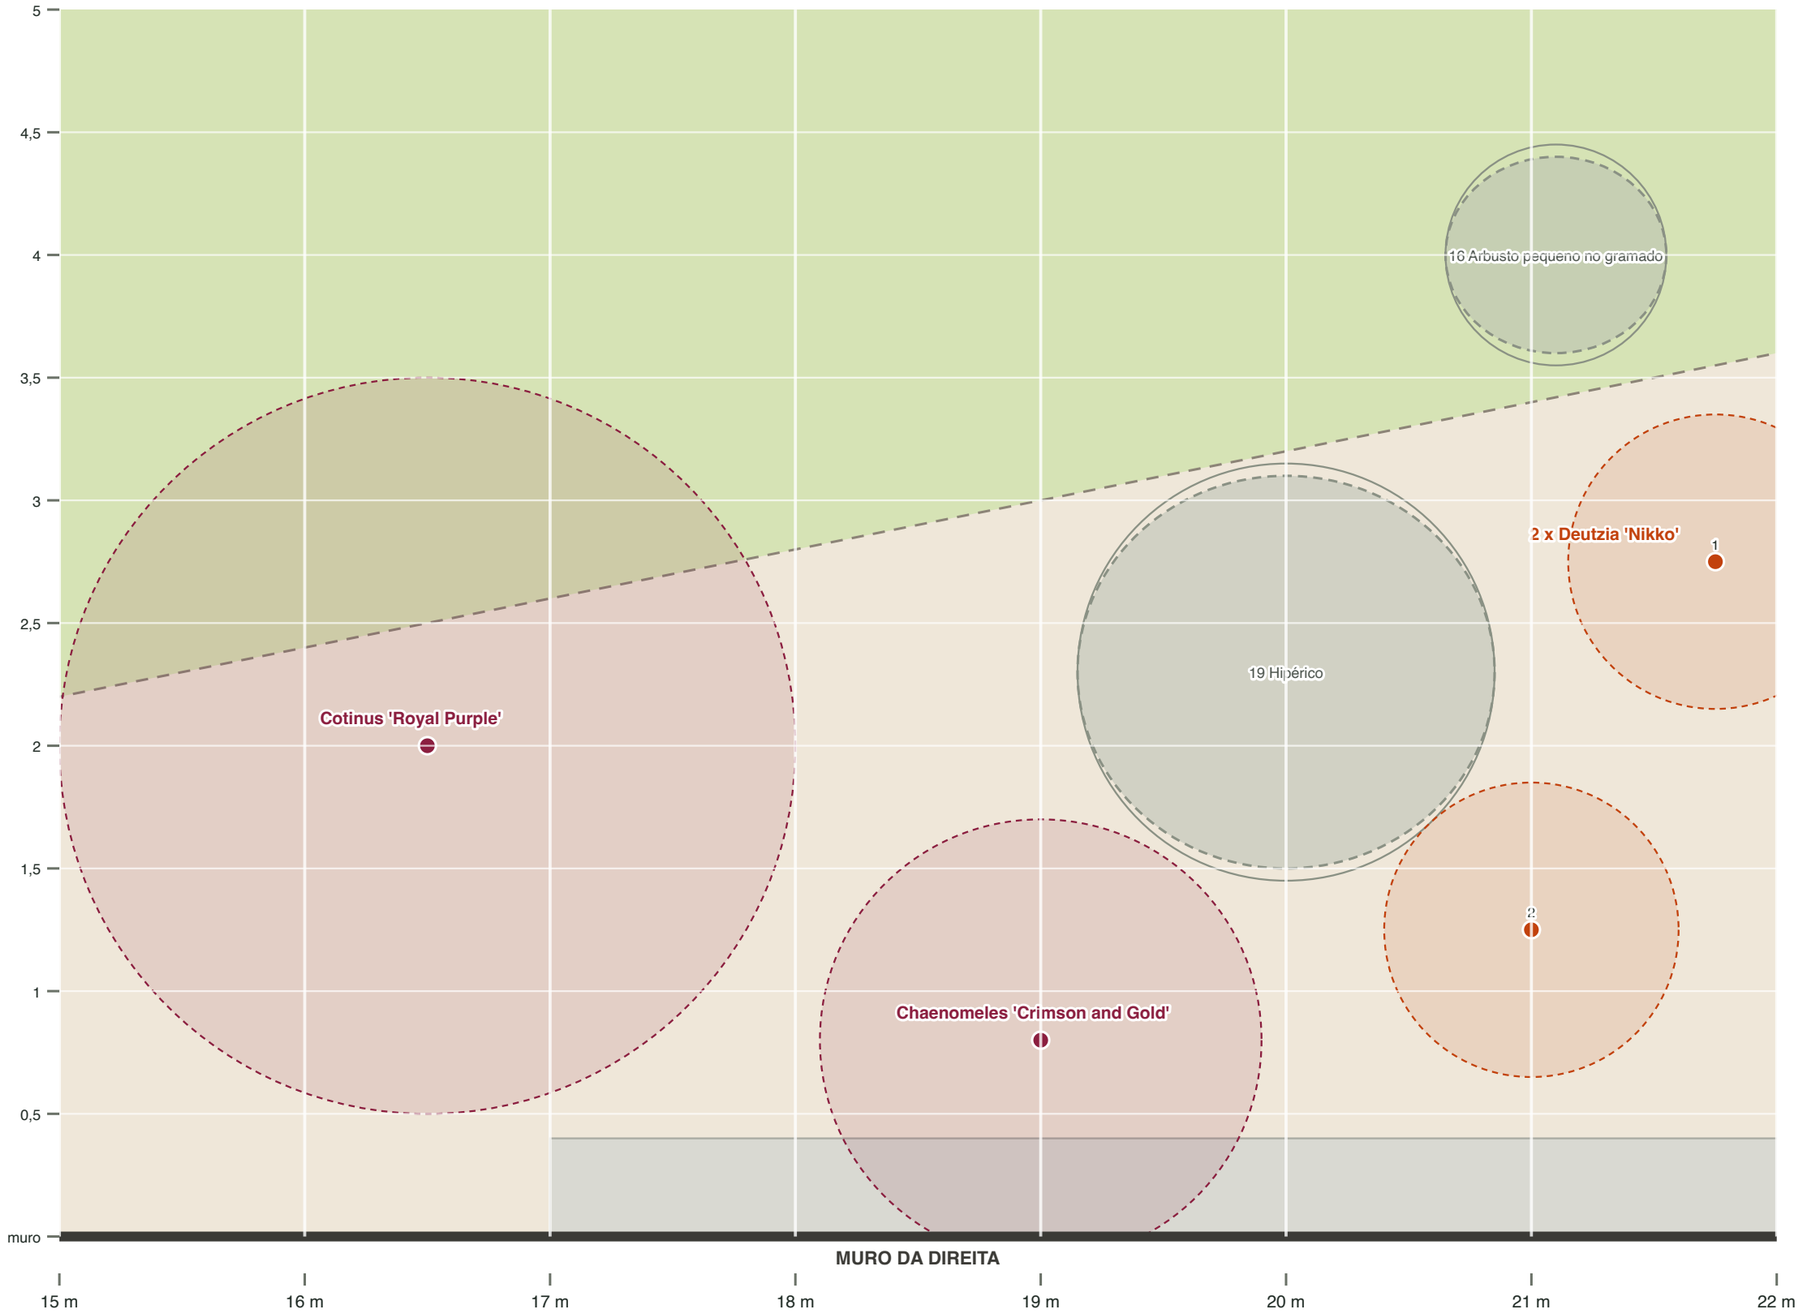


Metros a partir da casa, medidos ao longo do muro

**MARCAÇÃO: trena ao longo do muro, depois a partir do muro**

| | |
|---|---|
| **Cotinus 'Royal Purple'** | 16,5 ao longo, 2 do muro |
| **Chaenomeles 'Crimson and Gold'** | 19 ao longo, 0,8 do muro |
| **2 x Deutzia 'Nikko'** | |
| 1 | 21 ao longo, 1,25 do muro |
| 2 | 21,75 ao longo, 2,75 do muro |

**ANTES DE CAVAR**

As posições vêm de um levantamento por fotos, não de uma medição.
Coloque todos os vasos no lugar, caminhe pelos canteiros e só então cave.


# Canteiro da direita, de 22 a 29 m da casa



A casa fica à ESQUERDA desta folha e o bosque à DIREITA. O MURO DA DIREITA corre pela parte de BAIXO. Escala 1:25. Ponto = centro do vaso. Círculo claro = espaço de que a planta precisa.

< PARA A CASA

PARA O BOSQUE >

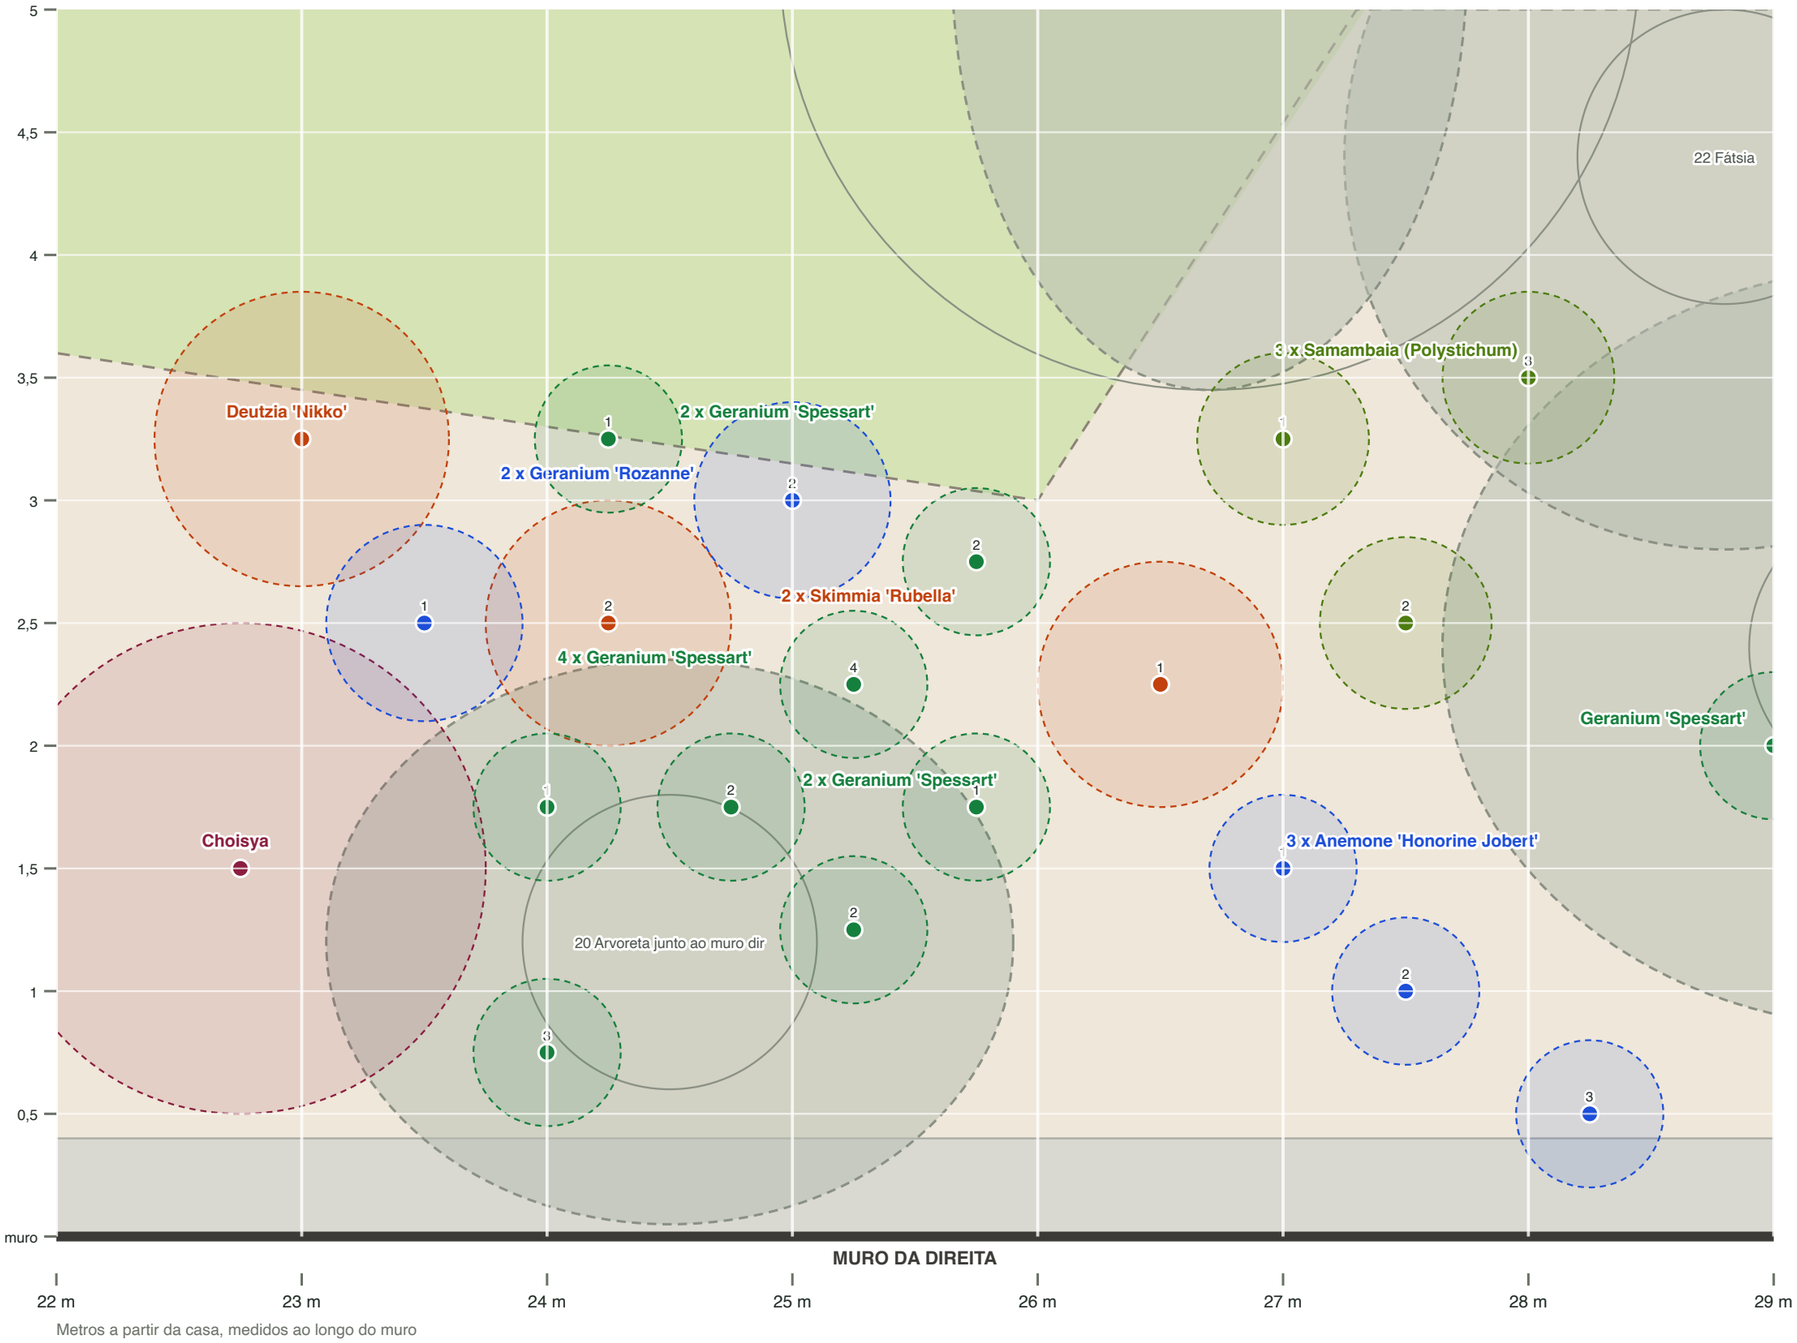


**MARCAÇÃO: trena ao longo do muro, depois a partir do muro**

| | |
|---|---|
| **Choisya** | 22,75 ao longo, 1,5 do muro |
| **Deutzia 'Nikko'** | 23 ao longo, 3,25 do muro |
| **2 x Geranium 'Rozanne'** | |
| 1 | 23,5 ao longo, 2,5 do muro |
| 2 | 25 ao longo, 3 do muro |
| **4 x Geranium 'Spessart'** | |
| 1 | 24 ao longo, 1,75 do muro |
| 2 | 24 ao longo, 0,75 do muro |
| 3 | 24,75 ao longo, 1,75 do muro |
| 4 | 25,25 ao longo, 2,25 do muro |
| **2 x Geranium 'Spessart'** | |
| 1 | 24,25 ao longo, 3,25 do muro |
| 2 | 25,75 ao longo, 2,75 do muro |
| **2 x Skimmia 'Rubella'** | |
| 1 | 24,25 ao longo, 2,5 do muro |
| 2 | 26,5 ao longo, 2,25 do muro |
| **2 x Geranium 'Spessart'** | |
| 1 | 25,25 ao longo, 1,25 do muro |
| 2 | 25,75 ao longo, 1,75 do muro |
| **3 x Samambaia (Polystichum)** | |
| 1 | 27 ao longo, 3,25 do muro |
| 2 | 27,5 ao longo, 2,5 do muro |
| 3 | 28 ao longo, 3,5 do muro |
| **3 x Anemone 'Honorine Jobert'** | |
| 1 | 27 ao longo, 1,5 do muro |
| 2 | 27,5 ao longo, 1 do muro |
| 3 | 28,25 ao longo, 0,5 do muro |
| **Geranium 'Spessart'** | 29 ao longo, 2 do muro |

**ANTES DE CAVAR**

As posições vêm de um levantamento por fotos, não de uma medição.
Coloque todos os vasos no lugar, caminhe pelos canteiros e só então cave.


# Canteiro da direita, de 29 a 36 m da casa



A casa fica à ESQUERDA desta folha e o bosque à DIREITA. O MURO DA DIREITA corre pela parte de BAIXO. Escala 1:25. Ponto = centro do vaso. Círculo claro = espaço de que a planta precisa.

< PARA A CASA

PARA O BOSQUE >

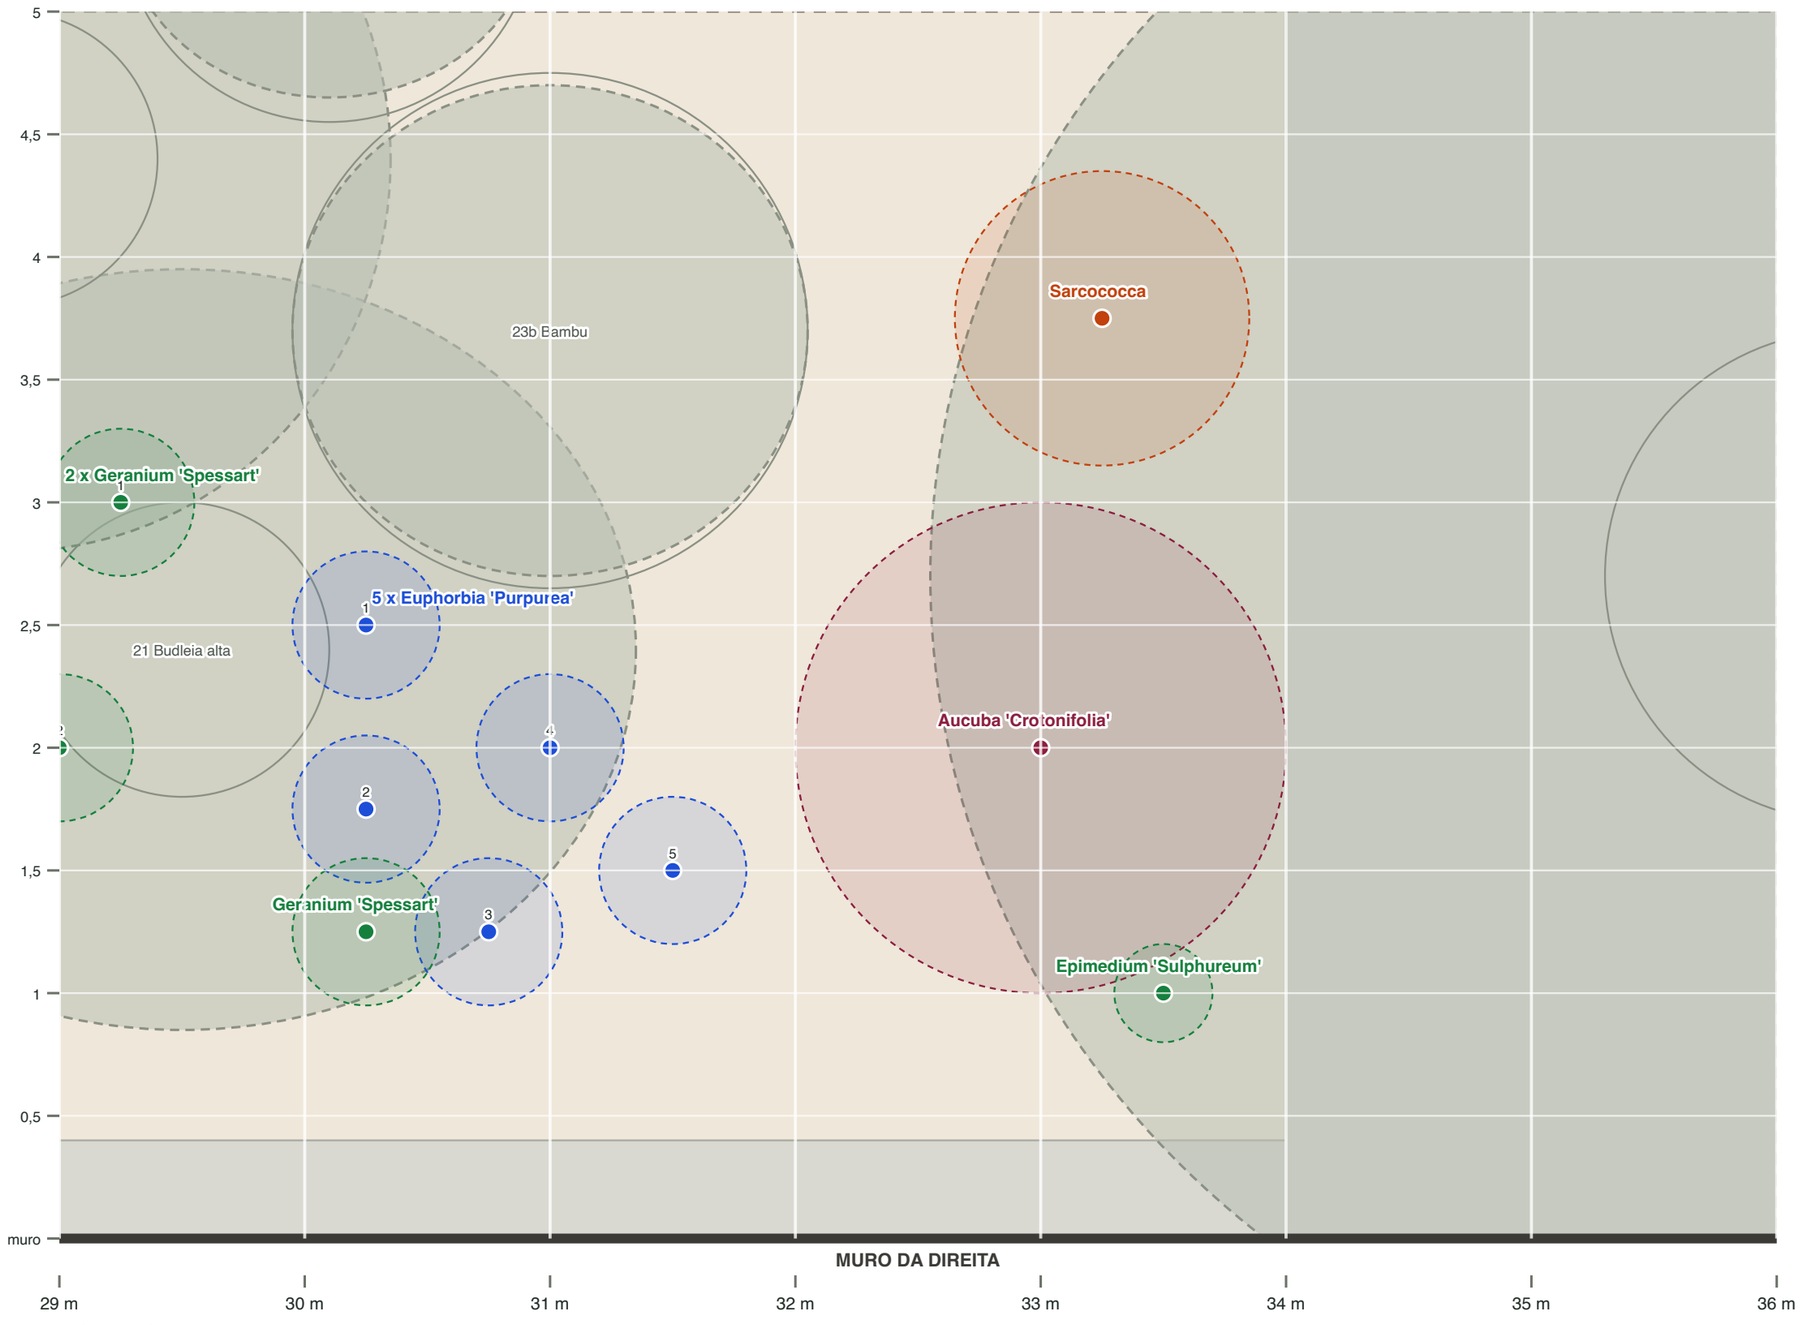


**MARCAÇÃO: trena ao longo do muro, depois a partir do muro**

| | |
|---|---|
| **2 x Geranium 'Spessart'** | |
| 1 | 29 ao longo, 2 do muro |
| 2 | 29,25 ao longo, 3 do muro |
| **5 x Euphorbia 'Purpurea'** | |
| 1 | 30,25 ao longo, 2,5 do muro |
| 2 | 30,25 ao longo, 1,75 do muro |
| 3 | 30,75 ao longo, 1,25 do muro |
| 4 | 31 ao longo, 2 do muro |
| 5 | 31,5 ao longo, 1,5 do muro |
| **Geranium 'Spessart'** | 30,25 ao longo, 1,25 do muro |
| **Aucuba 'Crotonifolia'** | 33 ao longo, 2 do muro |
| **Sarcococca** | 33,25 ao longo, 3,75 do muro |
| **Epimedium 'Sulphureum'** | 33,5 ao longo, 1 do muro |

**ANTES DE CAVAR**


As posições vêm de um levantamento por fotos, não de uma medição.
Coloque todos os vasos no lugar, caminhe pelos canteiros e só então cave.

# Bosque dos fundos e canteiros da casa




Escala 1:68. Casa embaixo em cada painel. O gramado e os canteiros entre 3,5 m e 31 m estão nas folhas 2 a 9.

**BOSQUE DOS FUNDOS, os últimos 12 m antes do muro do fundo (31 a 43 m da casa)**

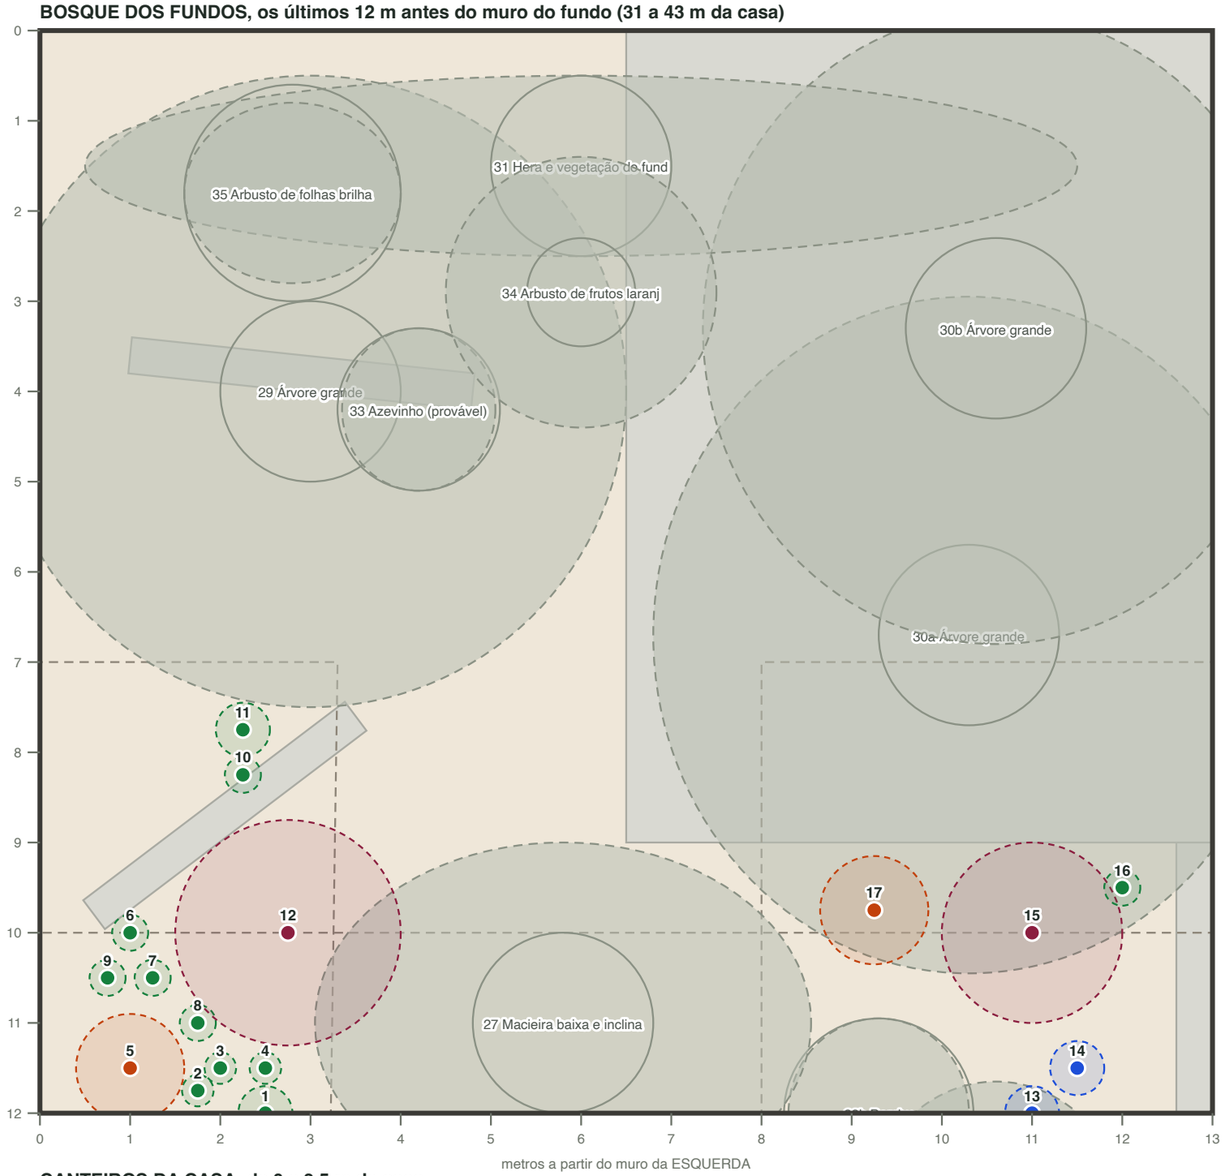


**CANTEIROS DA CASA, de 0 a 3,5 m da casa**

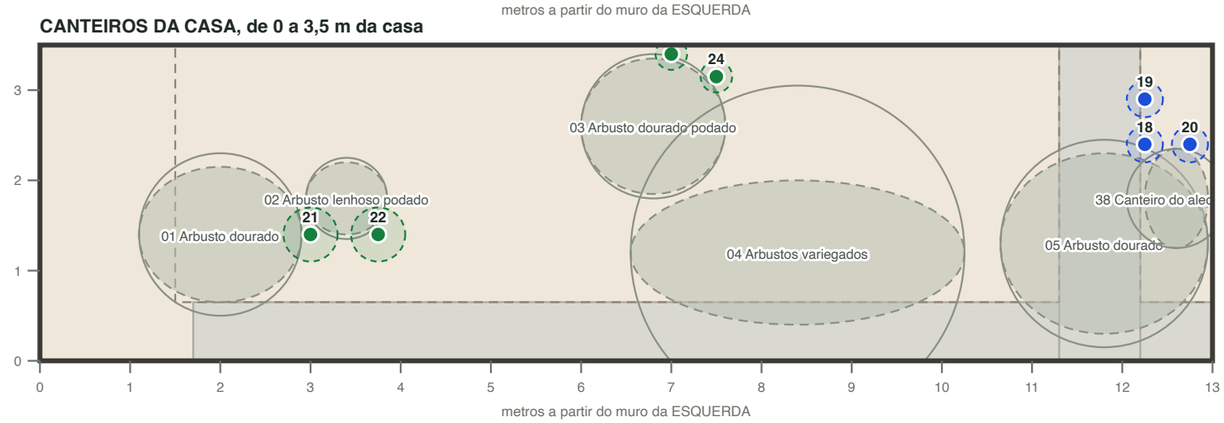


Gerado em 2026-11-05 a partir do levantamento fotográfico (rev. 04) e do pedido de 129 plantas da Palmstead.

**MARCAÇÃO: fundo = do MURO DO FUNDO; casa = da casa; depois do muro da esquerda**

| | |
|---|---|
| 1 Geranium 'Spessart' | 12 do muro do fundo, 2,5 do muro da esquerda |
| 2 Liriope | 11,75 do muro do fundo, 1,75 do muro da esquerda |
| 3 Liriope | 11,5 do muro do fundo, 2 do muro da esquerda |
| 4 Liriope | 11,5 do muro do fundo, 2,5 do muro da esquerda |
| 5 Sarcococca | 11,5 do muro do fundo, 1 do muro da esquerda |
| 6 Epimedium 'Sulphureum' | 10 do muro do fundo, 1 do muro da esquerda |
| 7 Epimedium 'Sulphureum' | 10,5 do muro do fundo, 1,25 do muro da esquerda |
| 8 Epimedium 'Sulphureum' | 11 do muro do fundo, 1,75 do muro da esquerda |
| 9 Epimedium 'Sulphureum' | 10,5 do muro do fundo, 0,75 do muro da esquerda |
| 10 Epimedium 'Sulphureum' | 8,25 do muro do fundo, 2,25 do muro da esquerda |
| 11 Geranium 'Spessart' | 7,75 do muro do fundo, 2,25 do muro da esquerda |
| 12 Osmanthus | 10 do muro do fundo, 2,75 do muro da esquerda |
| 13 Euphorbia 'Purpurea' | 12 do muro do fundo, 11 do muro da esquerda |
| 14 Euphorbia 'Purpurea' | 11,5 do muro do fundo, 11,5 do muro da esquerda |
| 15 Aucuba 'Crotonifolia' | 10 do muro do fundo, 11 do muro da esquerda |
| 16 Epimedium 'Sulphureum' | 9,5 do muro do fundo, 12 do muro da esquerda |
| 17 Sarcococca | 9,75 do muro do fundo, 9,25 do muro da esquerda |
| 18 Bergenia 'Bressingham White' | 2,4 da casa, 12,25 do muro da esquerda |
| 19 Bergenia 'Bressingham White' | 2,9 da casa, 12,25 do muro da esquerda |
| 20 Bergenia 'Bressingham White' | 2,4 da casa, 12,75 do muro da esquerda |
| 21 Geranium 'Spessart' | 1,4 da casa, 3 do muro da esquerda |
| 22 Geranium 'Spessart' | 1,4 da casa, 3,75 do muro da esquerda |
| 23 Liriope | 3,4 da casa, 7 do muro da esquerda |
| 24 Liriope | 3,15 da casa, 7,5 do muro da esquerda |

**FUNDO À DIREITA, ATRÁS DO BAMBU**

Há ali uma cerca viva e um caminho que não estão neste plano.
Mantenha o caminho livre. Plante só onde dá para cavar com a mão, entre as raízes.

**ANTES DE CAVAR**

As posições vêm de um levantamento por fotos, não de uma medição.
Coloque todos os vasos no lugar, caminhe pelos canteiros e só então cave.

# Conferência e decisões pendentes



Confira a entrega com esta lista antes de marcar.

## CONFERÊNCIA POR VARIEDADE

| Planta | Pedido | No plano | Vaso |
|---|---|---|---|
| Anemone × hybrida 'Honorine Jobert' | 3 | 3 | 2 L |
| Artemisia 'Powis Castle' | 3 | 3 | 2 L |
| Aucuba japonica 'Crotonifolia' | 2 | 2 | 10 L |
| Bergenia 'Bressingham White' | 5 | 5 | 2 L |
| Calamagrostis brachytricha | 5 | 5 | 2 L |
| Chaenomeles × superba 'Crimson & Gold' | 2 | 2 | 2 L |
| Choisya ternata | 1 | 1 | 7,5 L |
| Cotinus coggygria 'Royal Purple' | 1 | 1 | 25 L |
| Deutzia gracilis 'Nikko' | 9 | 9 | 2 L |
| Epimedium × versicolor 'Sulphureum' | 16 | 16 | 2 L |
| Euphorbia amygdaloides 'Purpurea' | 5 | 5 | 2 L |
| Geranium 'Rozanne' | 6 | 6 | 2 L |
| Geranium macrorrhizum 'Spessart' | 37 | 37 | 2 L |
| Liriope muscari | 5 | 5 | 2 L |
| Nepeta racemosa 'Walker's Low' | 6 | 6 | 2 L |
| Osmanthus × burkwoodii | 1 | 1 | 5 L |
| Philadelphus 'Virginal' | 1 | 1 | 25 L |
| Salvia nemorosa 'Caradonna' | 5 | 5 | 2 L |
| Sarcococca confusa | 3 | 3 | 4 L |
| Skimmia japonica 'Rubella' | 3 | 3 | 2 L |
| Polystichum setiferum | 5 | 5 | 2 L |
| Spiraea japonica 'Goldflame' | 3 | 3 | 1,5 L |
| Viburnum × bodnantense 'Dawn' | 1 | 1 | 10 L |
| Viburnum tinus 'Eve Price' | 1 | 1 | 2 L |
| **Total** | **129** | **129** | |

## VASOS POR CANTEIRO

| | |
|---|---|
| canteiro da esquerda | 73 |
| canteiro da direita | 45 |
| bosque dos fundos | 4 |
| canteiro da casa, à esquerda da escada | 4 |
| canteiro do alecrim, junto à escada | 3 |

## DECISÕES PENDENTES (em inglês, para o proprietário)

G04-3 Skimmia 'Rubella' moved 15.38 m along the bed to find part-or-shade; confirm or override.

K01-1 Aucuba 'Crotonifolia' at (11, 33) is in the pocket behind the bamboo; the hedge and the path there are not on the survey, keep the path clear.

K02-1 Epimedium 'Sulphureum' at (12, 33.5) is in the pocket behind the bamboo; the hedge and the path there are not on the survey, keep the path clear.

K04-1 Sarcococca at (9.25, 33.25) is in the pocket behind the bamboo; the hedge and the path there are not on the survey, keep the path clear.

## O QUE O PLANO PRESSUPÕE

O jardim tem 43 por 13 m, segundo a planta da imobiliária, não medido.
As bordas dos canteiros, o caminho e cada planta existente vêm de um levantamento por fotos (revisão 04, 24 de outubro de 2026).
O canteiro do alecrim e sua escada ficam na ponta direita da frente da casa, olhando para fora.
Os arbustos foram planejados no tamanho podado e podem avançar sobre o gramado, mas não sobre o caminho.
Plantas de sol só vão onde nada as sombreia; plantas de sombra nunca vão para o sol pleno.
Cada planta do pedido da Palmstead está no plano uma vez. Não há substituições.

## TRÊS COISAS DE QUE O PLANO DEPENDE

1. Pode a budleia junto ao terraço (17) e a budleia alta (21) até uns 60 cm todo mês de março, senão as plantas na frente delas vão ficar embaixo.

2. Mantenha o eleagno prateado grande (07) aparado na linha atual do lado do caminho; as Artemisia ao lado precisam de sol.

3. Teste o solo com um kit de pH antes de plantar as Skimmia e as Liriope. Se der acima de 7, plante em substrato para plantas acidófilas.

**ANTES DE CAVAR**

As posições vêm de um levantamento por fotos, não de uma medição.
Coloque todos os vasos no lugar, caminhe pelos canteiros e só então cave.